


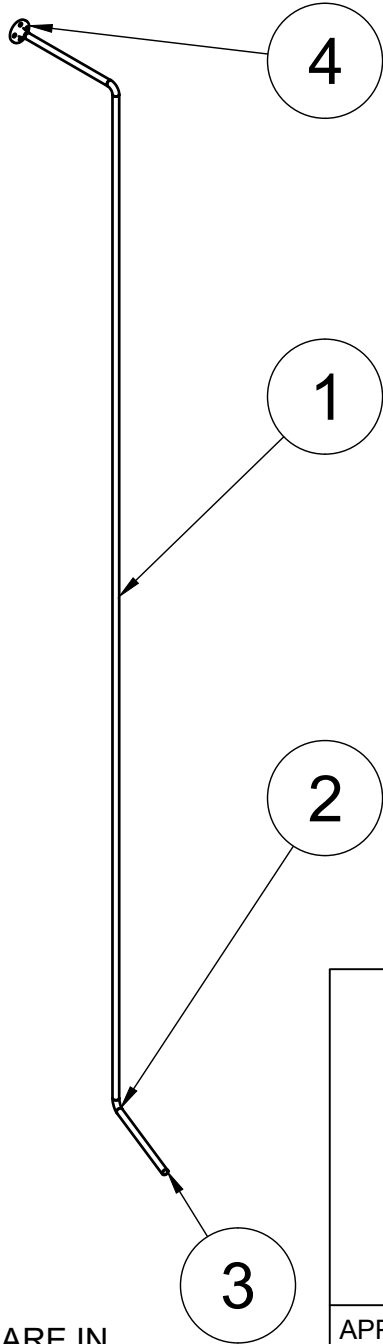

ALL UNITS ARE IN
INCHES



PARTS LIST			
ITEM	QTY	DESCRIPTION	MATERIAL
1	1	VERTICAL PIPE	STEEL ASTM A500 GR B
2	2	90 DEGREE FITTING	STEEL ASTM A500 GR B
3	2	HORIZONTAL PIPE	STEEL ASTM A500 GR B
4	1	PIPE FLANGE	STEEL ASTM A500 GR B

		PROJECT			
		Bulk Bag Unloader			
		TITLE			
		Air Lance			
APPROVED		SIZE	CODE	DWG NO	REV
CHECKED		A			
DRAWN	Jonathan Ganzer 4/10/2025	SCALE 1:30		WEIGHT	SHEET 1/5

NOTES:


For the two mirrored air lances, use an angle of -21.8° instead

All joints are to be welded

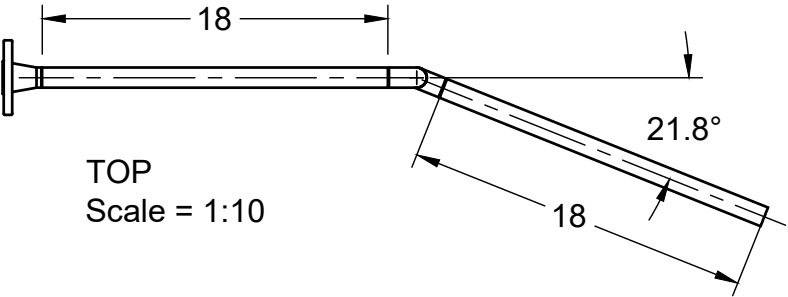
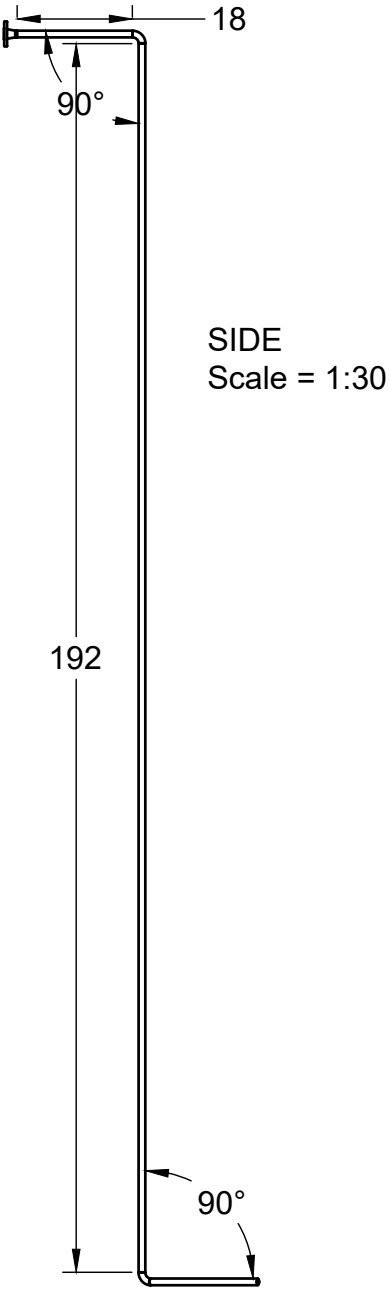


		PROJECT			
		Bulk Bag Unloader			
		TITLE			
		Air Lance			
APPROVED		SIZE	CODE	DWG NO	REV
CHECKED		A			
DRAWN	Jonathan Ganzer 4/10/2025	SCALE 1:30	WEIGHT	SHEET 2/5	

ALL UNITS ARE IN INCHES

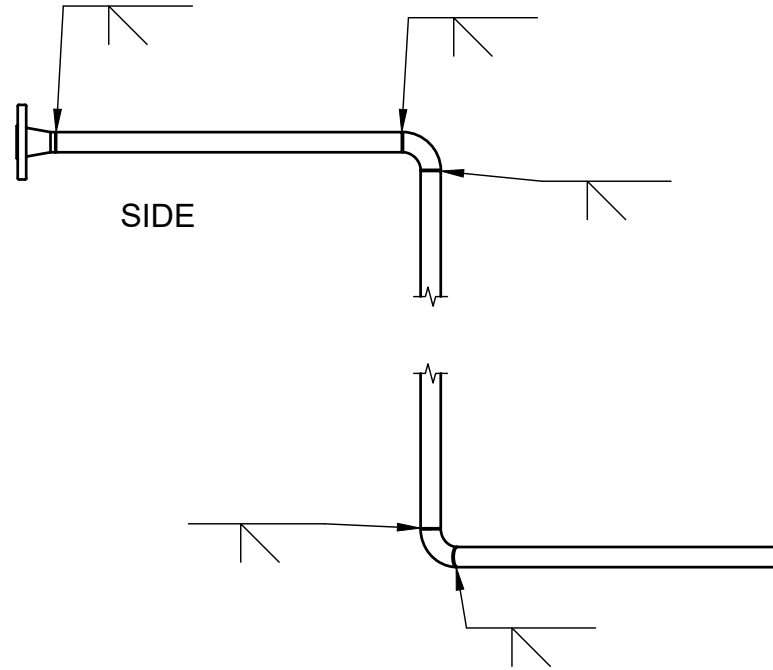


		PROJECT			
		Bulk Bag Unloader			
		TITLE			
		Air Lance - Welds			
APPROVED		SIZE	CODE	DWG NO	REV
CHECKED		A			
DRAWN	Jonathan Ganzer 4/10/2025	SCALE 1:10	WEIGHT	SHEET 3/5	

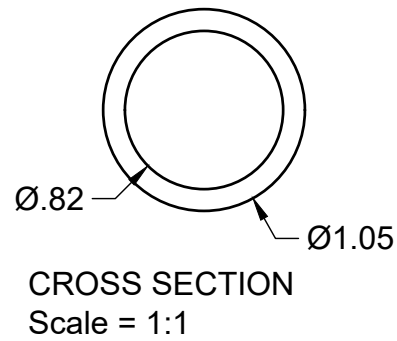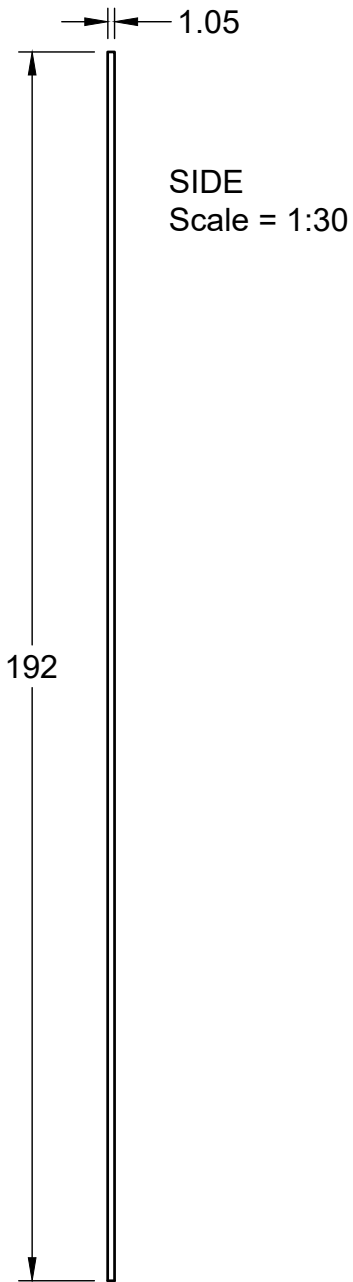


ALL UNITS ARE IN
INCHES

	PROJECT			
	Bulk Bag Unloader			
	TITLE			
	Vertical Pipe			
APPROVED	SIZE	CODE	DWG NO	REV
CHECKED	A			
DRAWN Jonathan Ganzer 4/10/2025	SCALE 1:30	WEIGHT	SHEET 4/5	

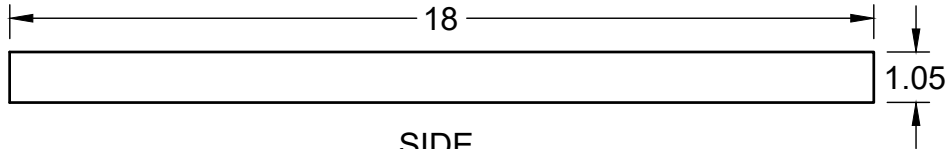




SIDE
Scale = 1:4

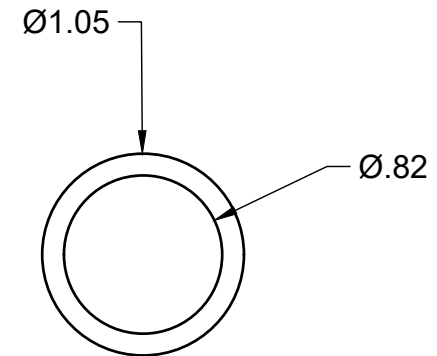

CROSS-SECTION
Scale = 1:1

ALL UNITS ARE IN
INCHES

	PROJECT			
	Bulk Bag Unloader			
	TITLE			
	Horizontal Pipe			
APPROVED	SIZE	CODE	DWG NO	REV
CHECKED	A			
DRAWN	Jonathan Ganzer	4/10/2025	SCALE 1:20	WEIGHT
				SHEET 5/5

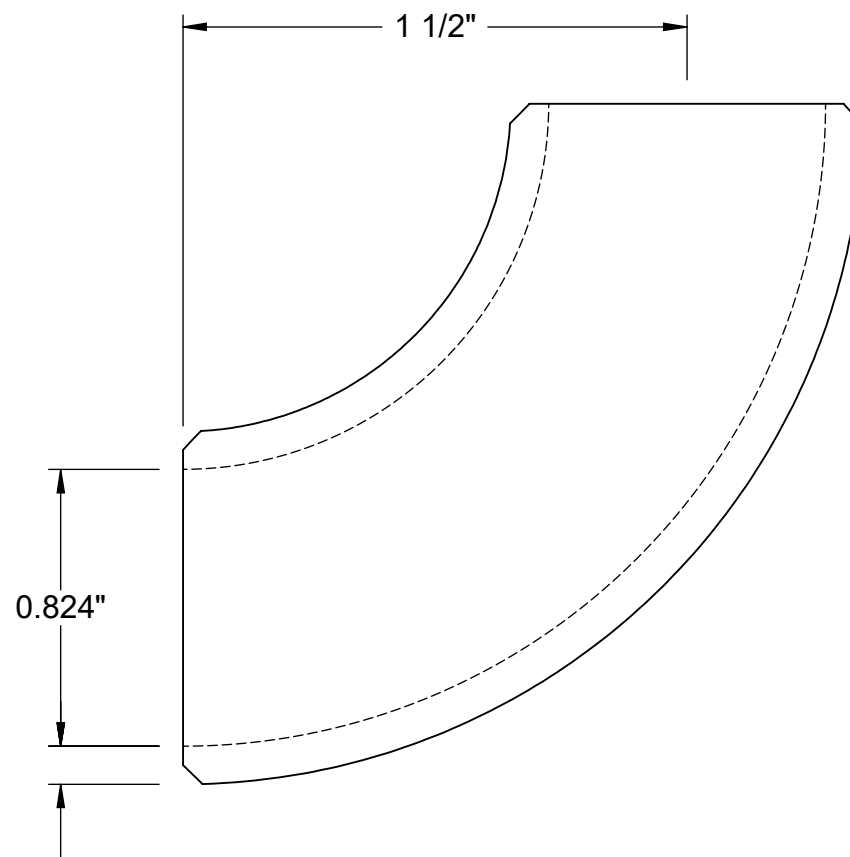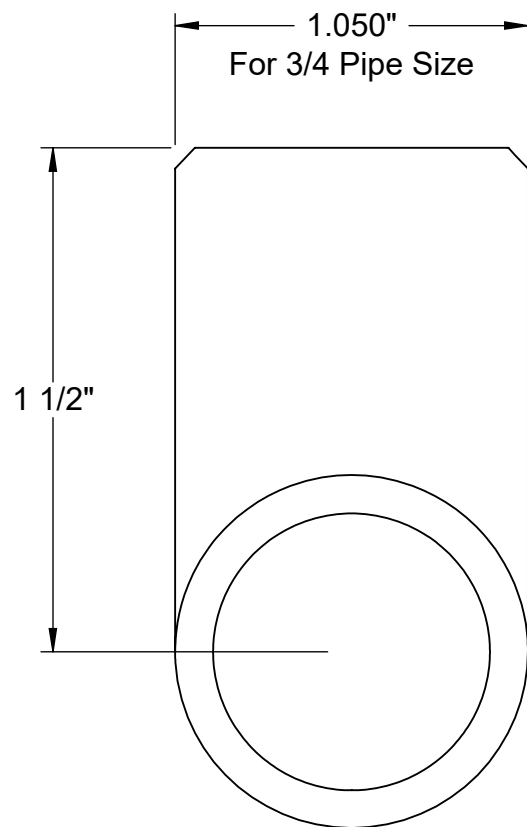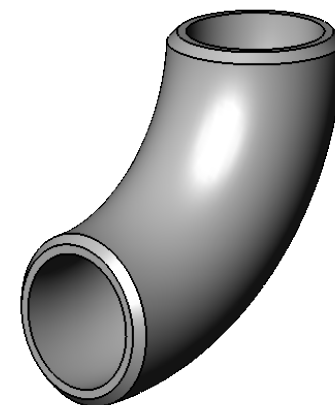

0.113"
Wall Thickness




McMASTER-CARR® 

<http://www.mcmaster.com>
© 2021 McMaster-Carr Supply Company

Information in this drawing is provided for reference only.

PART NUMBER **43425K121**

Standard-Wall Butt-Weld
Steel Unthreaded Fitting

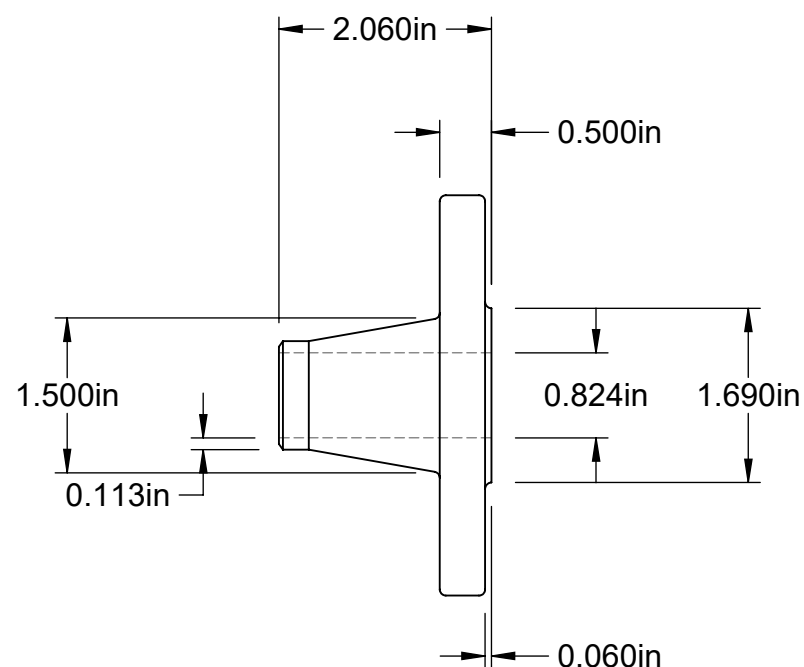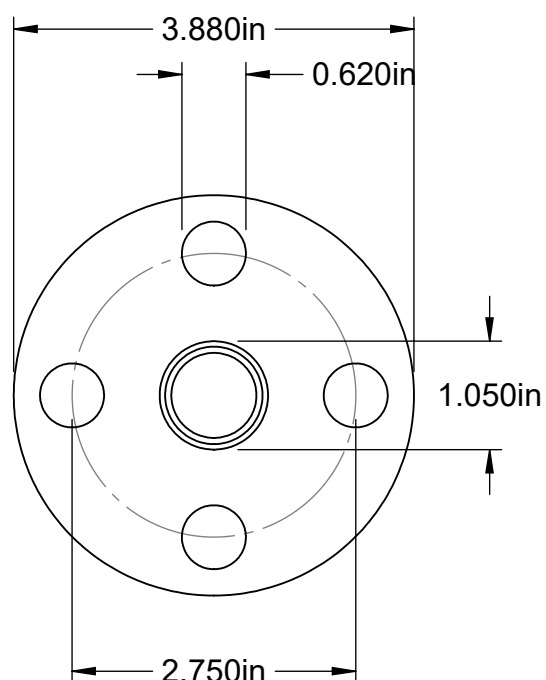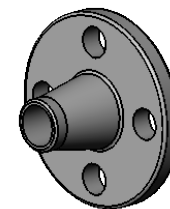

For Bolt Diameter: 0.500in
Pipe Size: 3/4

McMASTER-CARR®  http://www.mcmaster.com © 2023 McMaster-Carr Supply Company Information in this drawing is provided for reference only.	PART NUMBER 68095K364
	Low-Pressure Steel Unthreaded Pipe Flange