


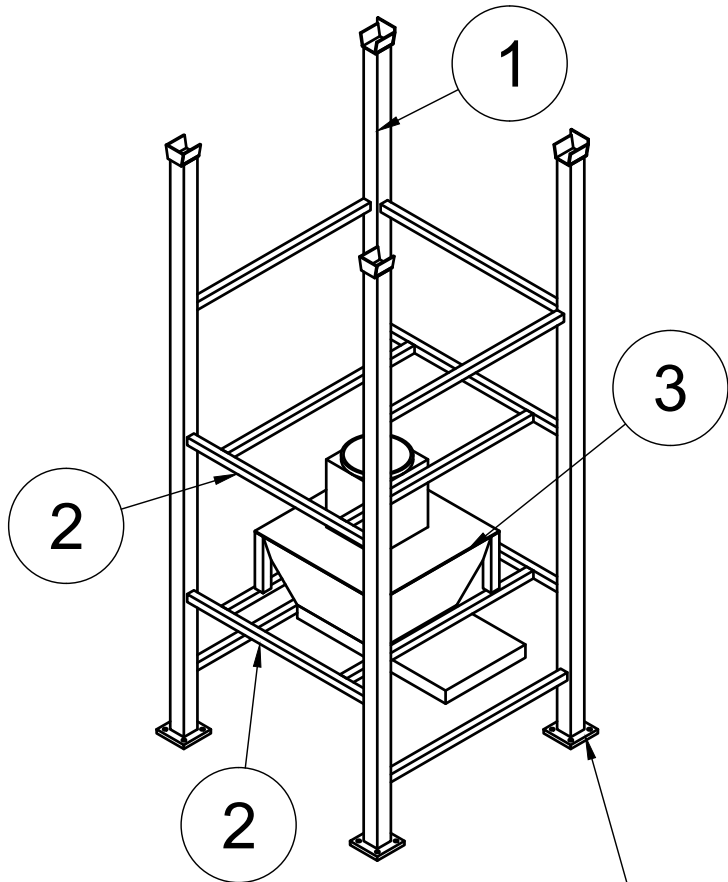

NOTES:



-Unless noted, all joints are to be welded

PARTS LIST		
ITEM	QTY	PART NAME
1	1	STRUCTURE
2	2	SUPPORT STRUCTURE
3	1	REUSED COMPONENTS V6

Will be bolted to existing pad hardware


ALL UNITS ARE IN INCHES

		PROJECT			
		Bulk Bag Unloader			
		TITLE			
		Unloading System			
APPROVED		SIZE	CODE	DWG NO	REV
CHECKED		A			
DRAWN	Jacob Ganzer	4/2/2025	SCALE 1:40	WEIGHT	SHEET 1/26

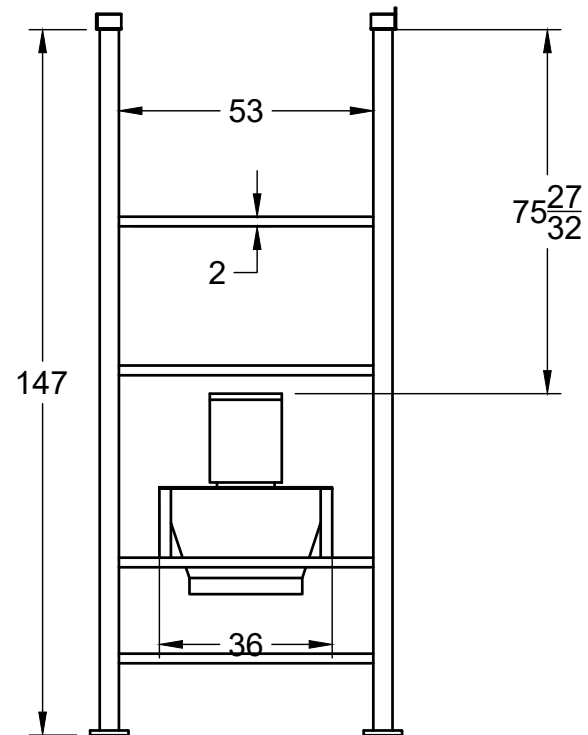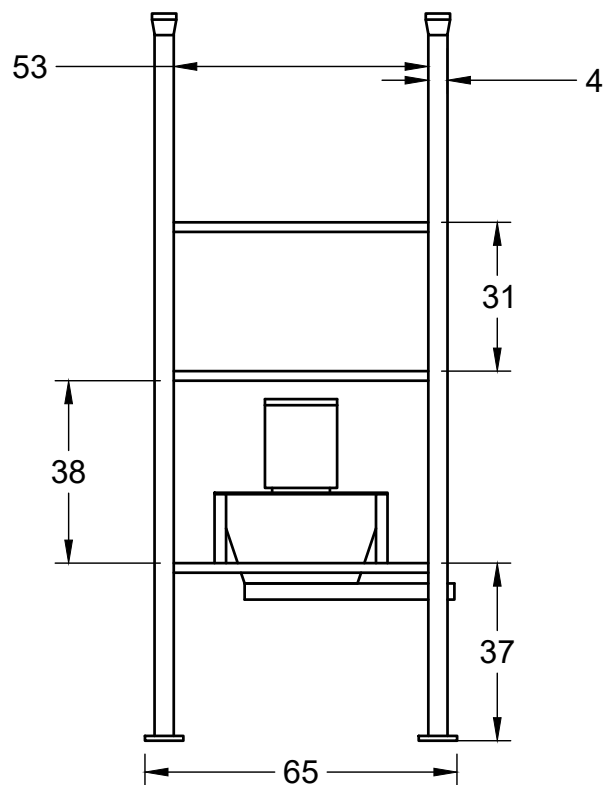

ALL UNITS ARE IN
INCHES


	PROJECT				
	Bulk Bag Unloader				
	TITLE				
	Unloading System				
APPROVED	SIZE A	CODE	DWG NO		REV
CHECKED					
DRAWN	Jacob Ganzer	4/2/2025	SCALE 1:40	WEIGHT	SHEET 2/26

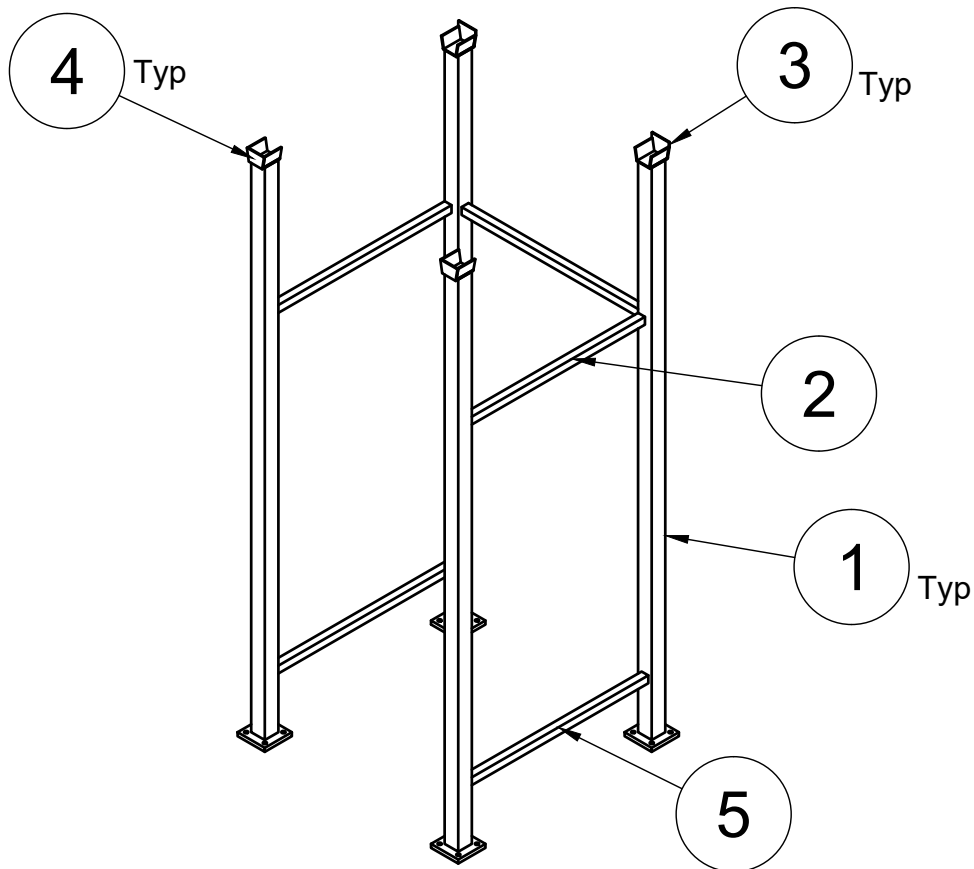

PARTS LIST		
ITEM	QTY	PART NAME
1	4	UPRIGHT STRUCTURE
2	1	BAG BRACE
3	2	UPRIGHT BACK CAP
4	2	UPRIGHT FRONT CAP
5	1	BASE BRACE

ALL UNITS ARE IN
INCHES


		PROJECT		
		Bulk Bag Unloader		
		TITLE		
		Structure		
APPROVED		SIZE	CODE	DWG NO
CHECKED		A		
DRAWN	Jacob Ganzer	4/2/2025	SCALE 1:60	WEIGHT
			SHEET 3/26	

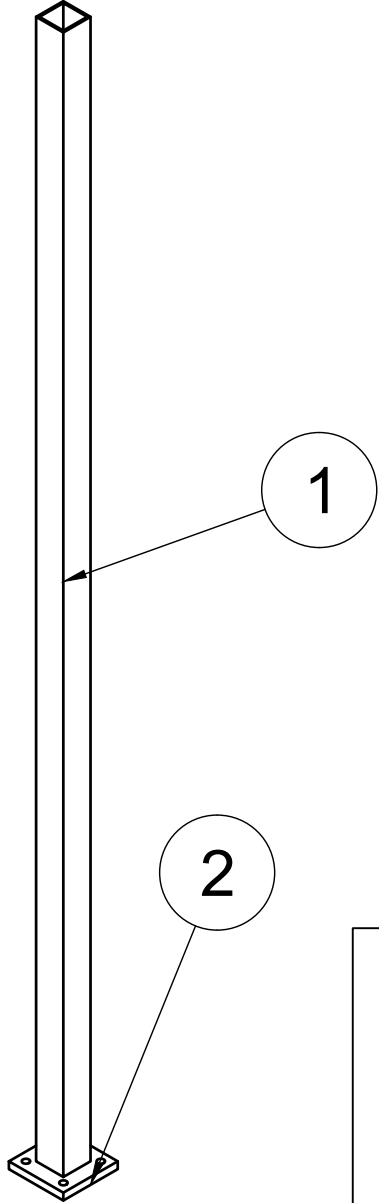

ALL UNITS ARE IN
INCHES


PARTS LIST				
ITEM	QTY	PART NAME	DESCRIPTION	MATERIAL
1	1	UPRIGHT SUPPORT	4"X4" TUBING	STEEL ASTM A500 GR B
2	1	BASE MOUNT	PLATE	STEEL ASTM A36

		PROJECT			
		Bulk Bag Unloader			
		TITLE			
		Upright Structure			
APPROVED		SIZE	CODE	DWG NO	REV
CHECKED		A			
DRAWN	Jacob Ganzer	4/2/2025	SCALE 1:20	WEIGHT	SHEET 4/26

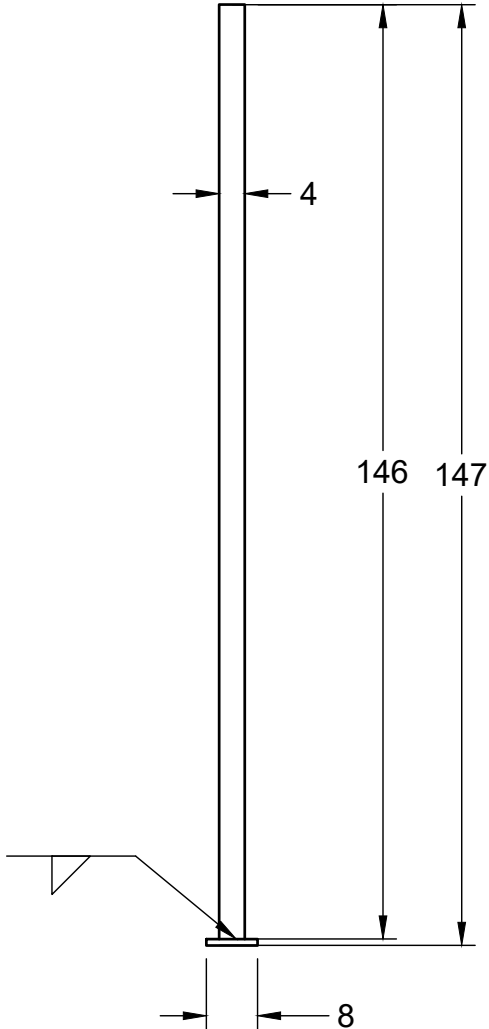


ALL UNITS ARE IN
INCHES

		PROJECT			
		Bulk Bag Unloader			
		TITLE			
		Upright Structure			
APPROVED		SIZE	CODE	DWG NO	REV
CHECKED		A			
DRAWN	Jacob Ganzer	4/2/2025	SCALE 1:20	WEIGHT	SHEET 5/26

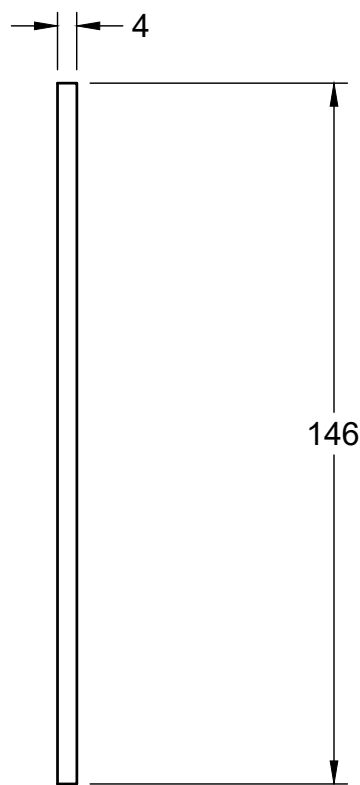



SCALE 1:40

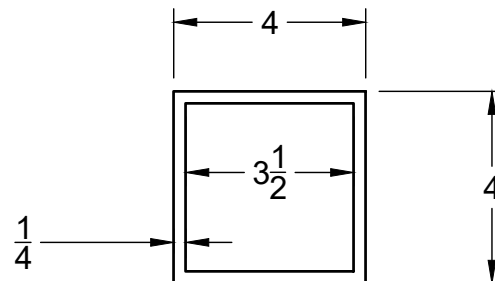

SCALE 1:4


ALL UNITS ARE IN
INCHES

		PROJECT			
		Bulk Bag Unloader			
		TITLE			
		Upright Support			
APPROVED		SIZE	CODE	DWG NO	REV
CHECKED		A			
DRAWN	Jacob Ganzer	4/2/2025	SCALE 1:40	WEIGHT	SHEET 6/26

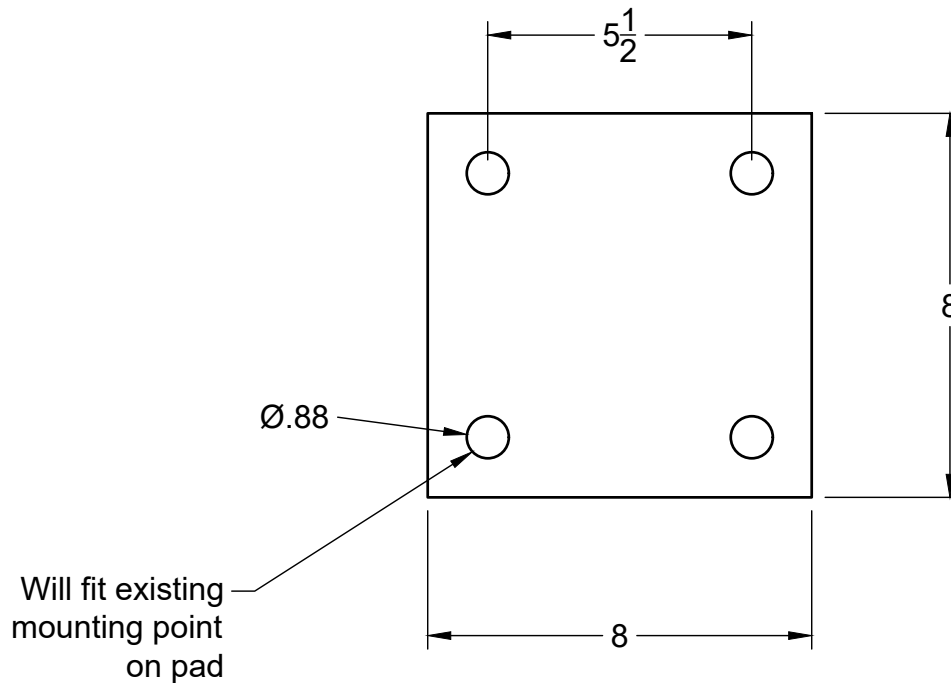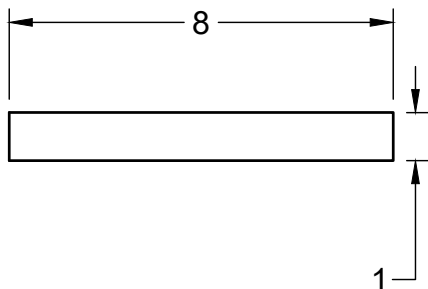

ALL UNITS ARE IN
INCHES

		PROJECT			
		Bulk Bag Unloader			
		TITLE			
		Upright Support Bottom			
APPROVED		SIZE	CODE	DWG NO	REV
CHECKED		A			
DRAWN	Jacob Ganzer	4/2/2025	SCALE 1:4	WEIGHT	SHEET 7/26

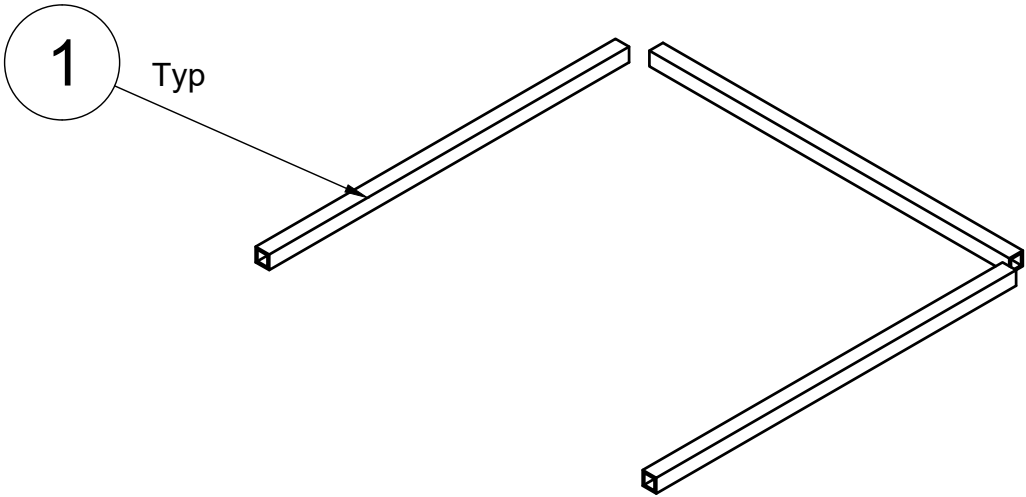

NOTES:

All joints are to be welded

PARTS LIST			
ITEM	QTY	PART NUMBER	MATERIAL
1	3	STRUCTURAL BAR C	STEEL ASTM A500 GR B


		PROJECT		
		Bulk Bag Unloader		
		TITLE		
		Bag Brace		
APPROVED		SIZE	CODE	DWG NO
CHECKED		A		
DRAWN	Jacob Ganzer	4/2/2025	SCALE 1:20	WEIGHT
				SHEET 8/26

ALL UNITS ARE IN INCHES



NOTES:

All joints are to be welded

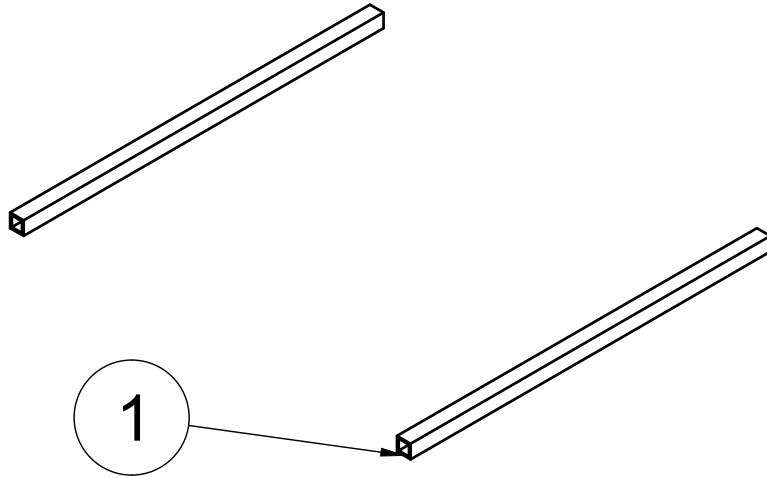


PARTS LIST			
ITEM	QTY	PART NUMBER	MATERIAL
1	2	STRUCTURAL BAR C	STEEL ASTM A500 GR B


		PROJECT		
		Bulk Bag Unloader		
		TITLE		
		Base Brace		
APPROVED		SIZE	CODE	DWG NO
CHECKED		A		
DRAWN	Jacob Ganzer	4/2/2025	SCALE 1:20	WEIGHT
				SHEET 9/26

ALL UNITS ARE IN
INCHES



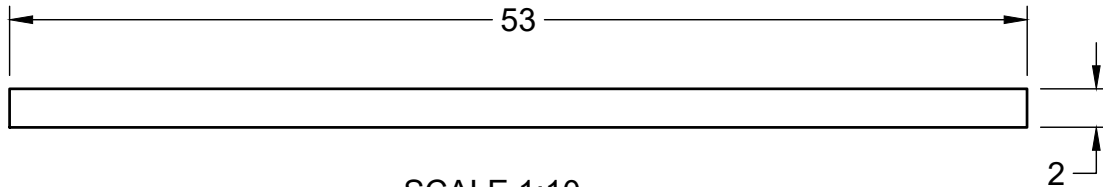


SCALE 1:10

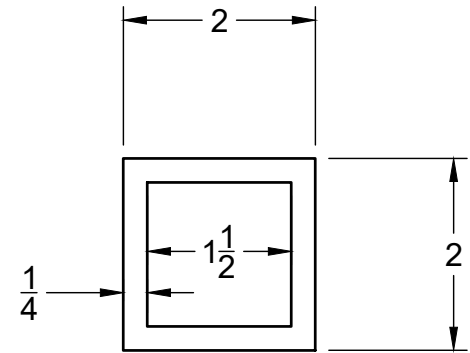

SCALE 1:2


ALL UNITS ARE IN
INCHES

				PROJECT			
				Bulk Bag Unloader			
				TITLE			
				Structural Bar C			
APPROVED				SIZE	CODE	DWG NO	REV
CHECKED				A			
DRAWN	Jacob Ganzer	4/2/2025	SCALE 1:10	WEIGHT		SHEET 10/26	

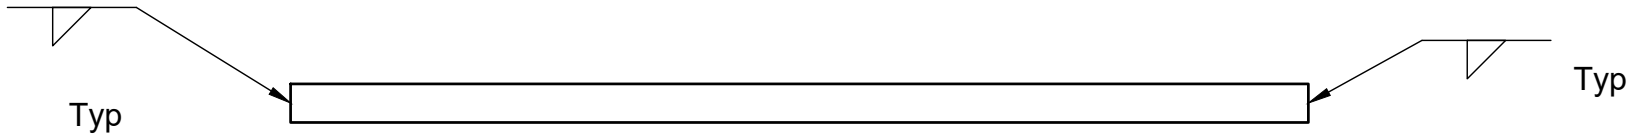

ALL UNITS ARE IN
INCHES

		PROJECT			
		Bulk Bag Unloader			
		TITLE			
		Structural Bar C			
APPROVED		SIZE	CODE	DWG NO	REV
CHECKED		A			
DRAWN	Jacob Ganzer	4/2/2025	SCALE 1:10	WEIGHT	SHEET 11/26

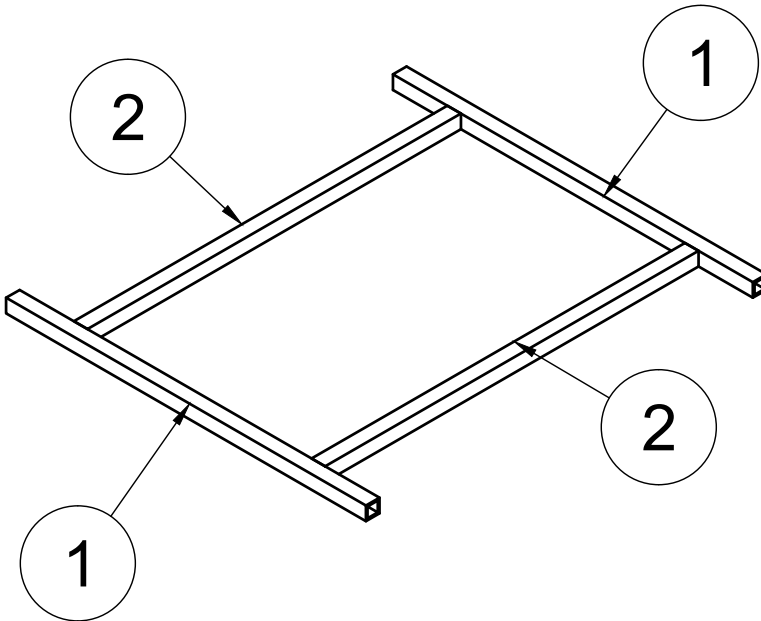


NOTES:

All joints are to be welded


PARTS LIST				
ITEM	QTY	PART NAME	DESCRIPTION	MATERIAL
1	2	STRUCTURAL BAR A	2"X2" TUBING	STEEL ASTM A500 GR B
2	2	STRUCTURAL BAR B	2"X2" TUBING	STEEL ASTM A500 GR B

		PROJECT			
		Bulk Bag Unloader			
		TITLE			
		Support Structure			
APPROVED		SIZE	CODE	DWG NO	REV
CHECKED		A			
DRAWN	Jacob Ganzer	4/2/2025	SCALE 1:20	WEIGHT	SHEET 12/26

ALL UNITS ARE IN INCHES

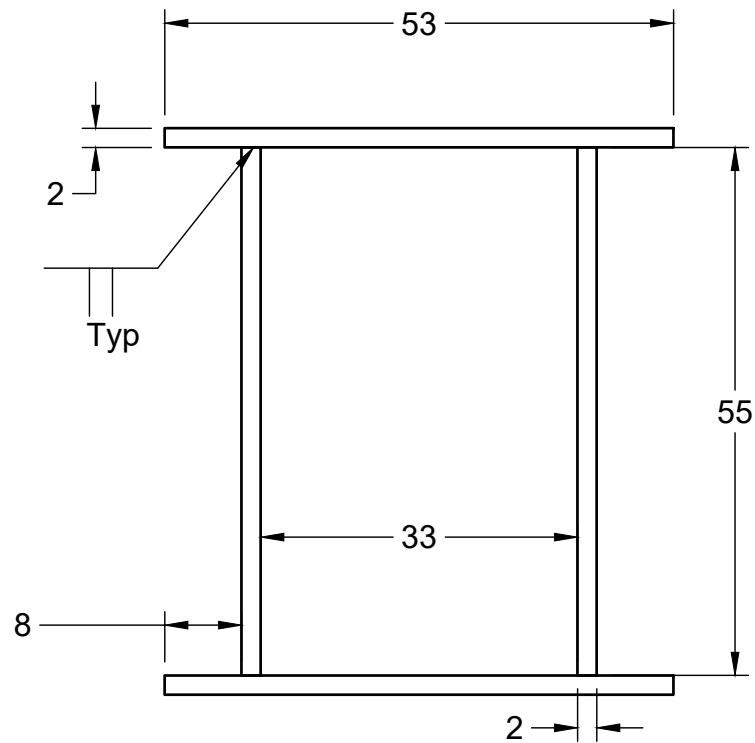



Top

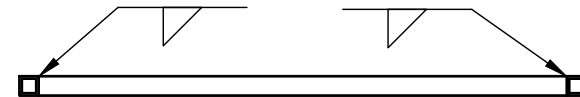

Side



ALL UNITS ARE IN
INCHES

				PROJECT			
				Bulk Bag Unloader			
				TITLE			
				Support Structure			
APPROVED				SIZE	CODE	DWG NO	REV
CHECKED				A			
DRAWN	Jacob Ganzer	4/2/2025	SCALE	1:20	WEIGHT	SHEET 13/26	

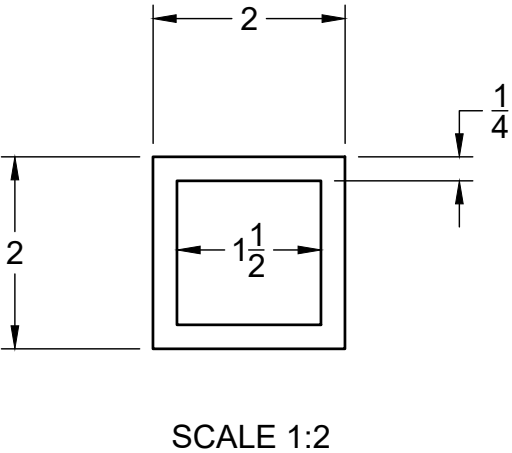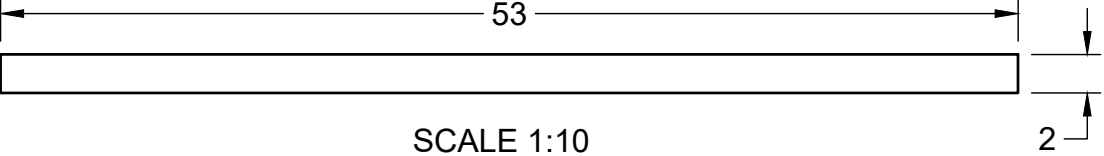


ALL UNITS ARE IN
INCHES

		PROJECT			
		Bulk Bag Unloader			
		TITLE			
		Structural Bar A			
APPROVED		SIZE	CODE	DWG NO	REV
CHECKED		A			
DRAWN	Jacob Ganzer	4/2/2025	SCALE 1:10	WEIGHT	SHEET 14/26

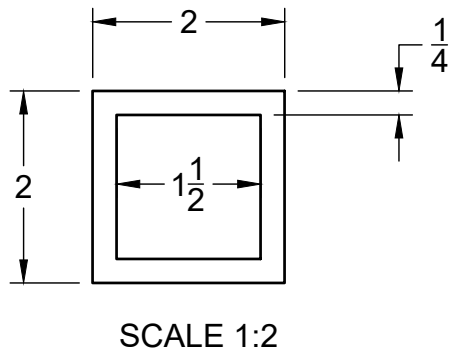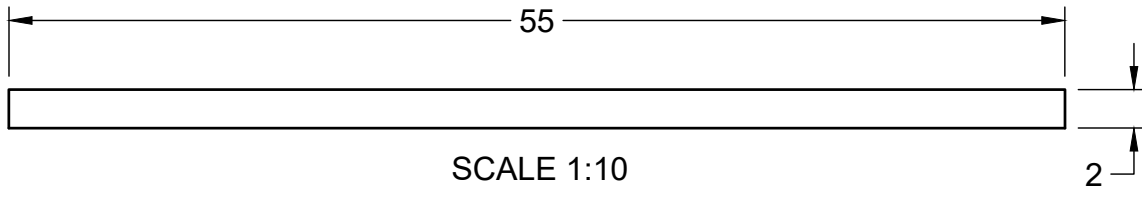

ALL UNITS ARE IN
INCHES

		PROJECT			
		Bulk Bag Unloader			
		TITLE			
		Structural Bar B			
APPROVED		SIZE	CODE	DWG NO	REV
CHECKED		A			
DRAWN	Jacob Ganzer	4/2/2025	SCALE 1:10	WEIGHT	SHEET 15/26

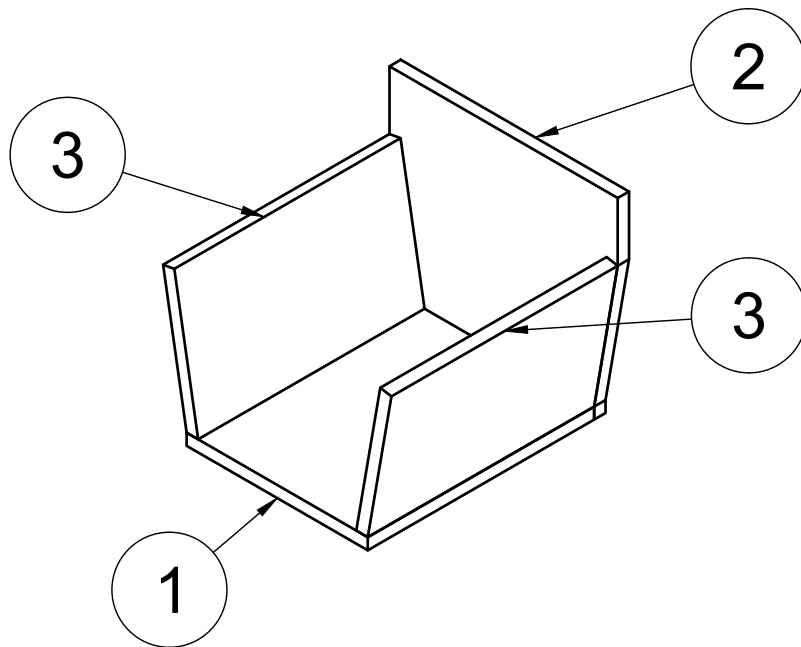

NOTES:

All joints are to be welded

PARTS LIST				
ITEM	QTY	PART NAME	DESCRIPTION	MATERIAL
1	1	CAP BASE	1/4" PLATE	STEEL ASTM A36
2	1	TALL BACK	1/4" PLATE	STEEL ASTM A36
3	2	CAP SIDE	1/4" PLATE	STEEL ASTM A36

PROJECT


Bulk Bag Unloader

TITLE


Upright Back Cap

ALL UNITS ARE IN
INCHES

APPROVED			SIZE A	CODE	DWG NO	REV
CHECKED						
DRAWN	Jacob Ganzer	4/2/2025	SCALE 1:3		WEIGHT	SHEET 16/26

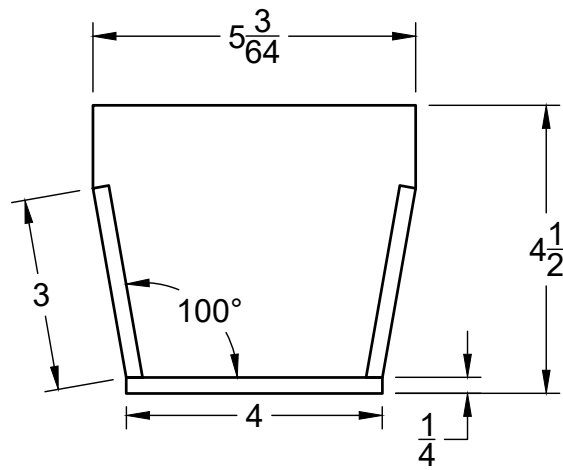


Front

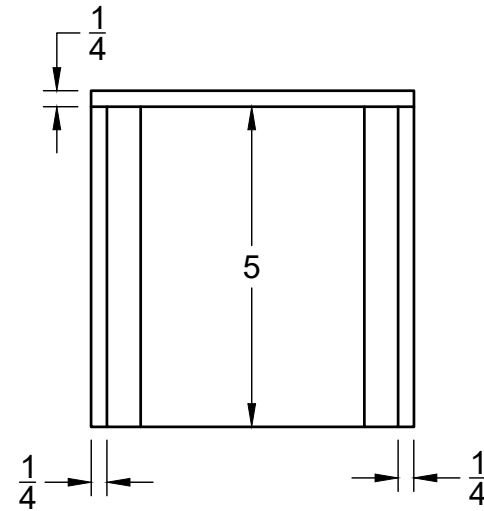


Top

ALL UNITS ARE IN
INCHES

		PROJECT			
		Bulk Bag Unloader			
		TITLE			
		Upright Back Cap			
APPROVED		SIZE	CODE	DWG NO	REV
CHECKED		A			
DRAWN	Jacob Ganzer	4/2/2025	SCALE 1:3	WEIGHT	SHEET 17/26

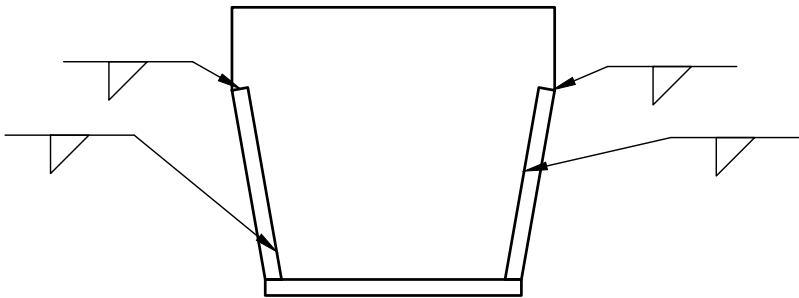


Front

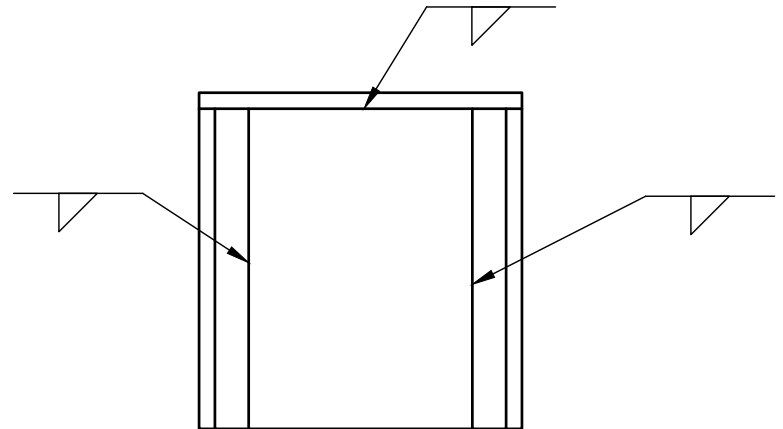

Top

ALL UNITS ARE IN
INCHES

		PROJECT			
		Bulk Bag Unloader			
		TITLE			
		Upright Back Cap			
APPROVED		SIZE	CODE	DWG NO	REV
CHECKED		A			
DRAWN	Jacob Ganzer	4/2/2025	SCALE 1:3	WEIGHT	SHEET 18/26

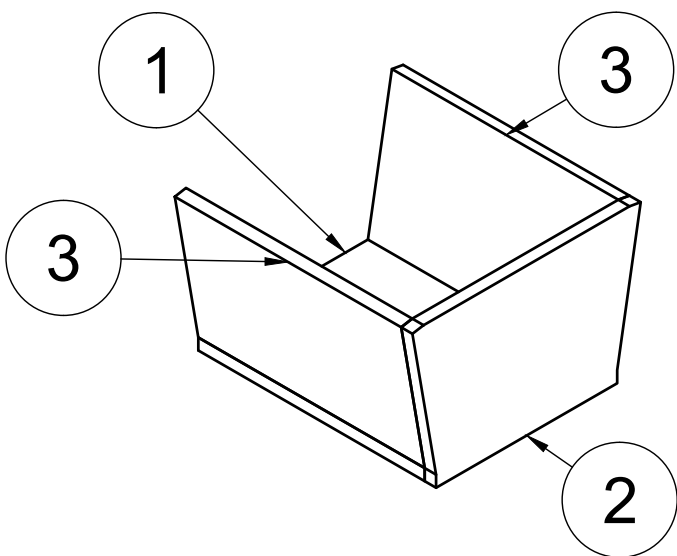


NOTES:

All joints are to be welded


PARTS LIST				
ITEM	QTY	PART NAME	DESCRIPTION	MATERIAL
1	1	CAP BASE	1/4" PLATE	STEEL ASTM A36
2	1	SHORT BACK	1/4" PLATE	STEEL ASTM A36
3	2	CAP SIDE	1/4" PLATE	STEEL ASTM A36

		PROJECT		
		Bulk Bag Unloader		
		TITLE		
		Upright Front Cap		
APPROVED		SIZE	CODE	DWG NO
CHECKED		A		
DRAWN	Jacob Ganzer	4/2/2025	SCALE 1:3	WEIGHT
			SHEET 19/26	

ALL UNITS ARE IN INCHES

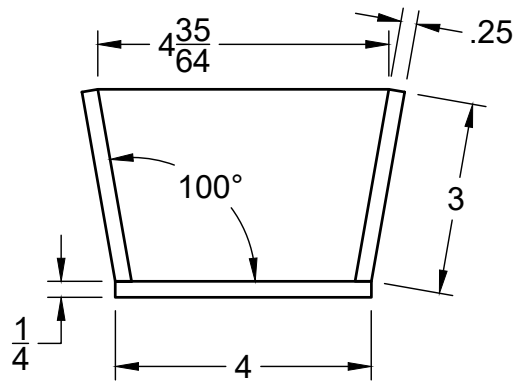


Front

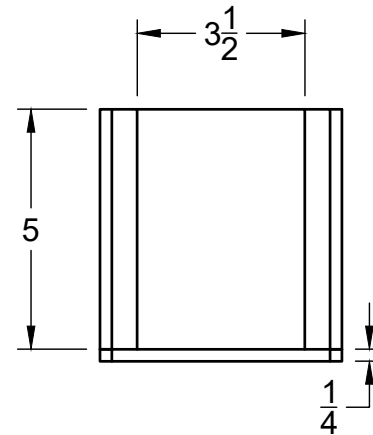


Top

ALL UNITS ARE IN
INCHES

		PROJECT			
		Bulk Bag Unloader			
		TITLE			
		Upright Front Cap			
APPROVED		SIZE	CODE	DWG NO	REV
CHECKED		A			
DRAWN	Jacob Ganzer	4/2/2025	SCALE 1:3	WEIGHT	SHEET 20/26

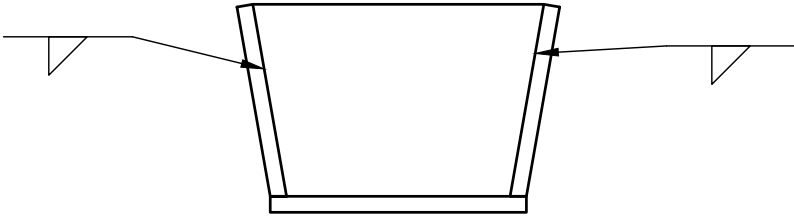


Front

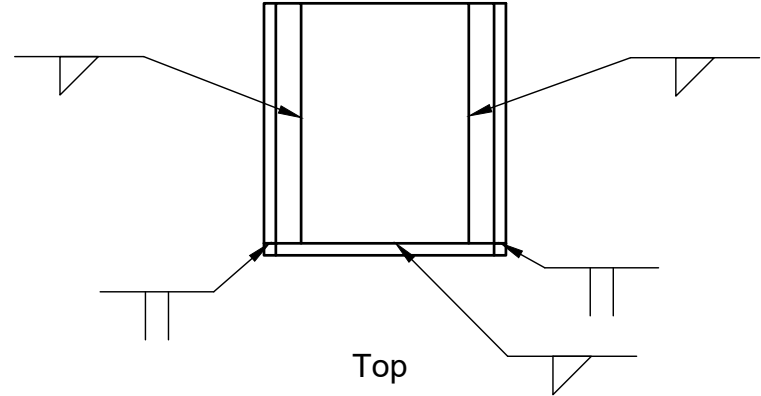


Top

ALL UNITS ARE IN
INCHES

	PROJECT				
	Bulk Bag Unloader				
	TITLE				
	Upright Front Cap				
APPROVED	SIZE A	CODE	DWG NO	REV	
CHECKED					
DRAWN	Jacob Ganzer	4/2/2025	SCALE 1:3	WEIGHT	SHEET 21/26

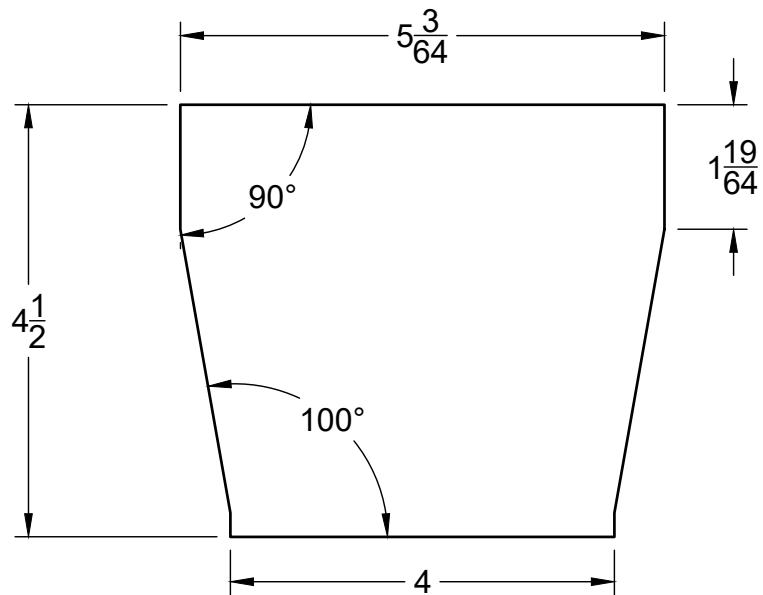


Front

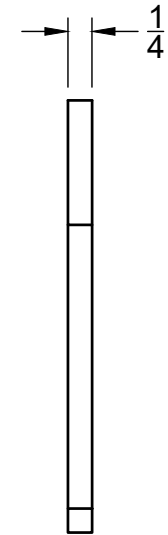


Side

ALL UNITS ARE IN
INCHES

		PROJECT			
		Bulk Bag Unloader			
		TITLE			
		Tall Back			
APPROVED		SIZE	CODE	DWG NO	REV
CHECKED		A			
DRAWN	Jacob Ganzer	4/2/2025	SCALE 1:2	WEIGHT	SHEET 22/26

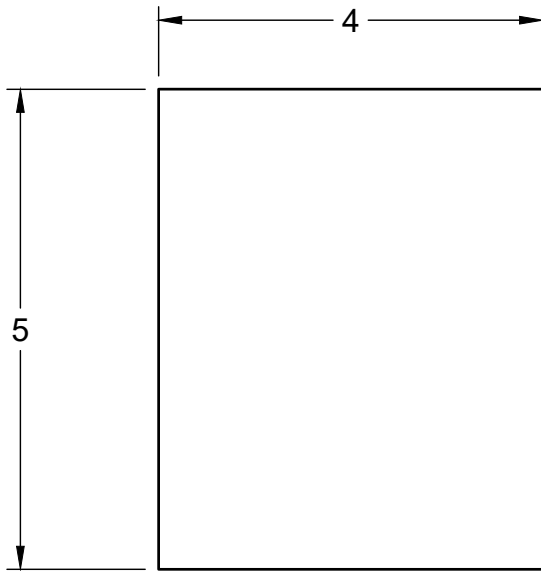


Top

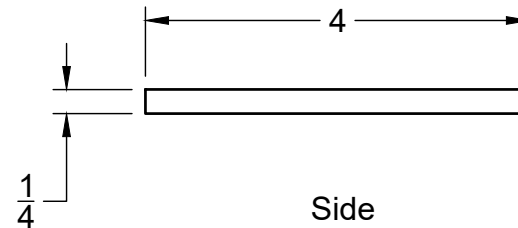


Side

ALL UNITS ARE IN
INCHES

				PROJECT			
				Bulk Bag Unloader			
				TITLE			
				Cap Base			
APPROVED				SIZE	CODE	DWG NO	REV
CHECKED				A			
DRAWN	Jacob Ganzer	4/2/2025	SCALE	1:2	WEIGHT	SHEET 23/26	

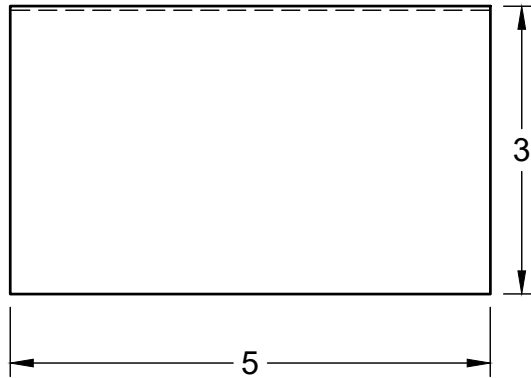


Bottom

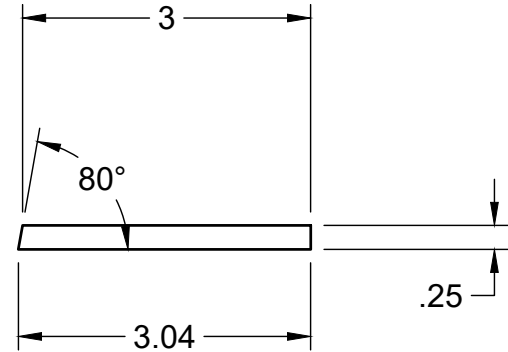


Side

ALL UNITS ARE IN
INCHES

				PROJECT			
				Bulk Bag Unloader			
				TITLE			
				Cap Side			
APPROVED				SIZE	CODE	DWG NO	REV
CHECKED				A			
DRAWN	Jacob Ganzer	4/2/2025	SCALE	1:2	WEIGHT	SHEET 24/26	

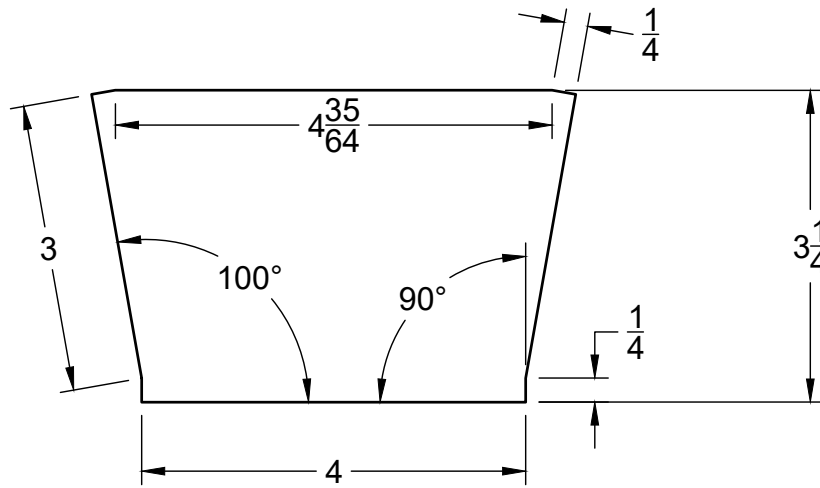


Front

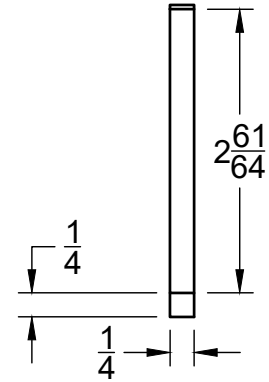

Side

ALL UNITS ARE IN
INCHES

		PROJECT			
		Bulk Bag Unloader			
		TITLE			
		Short Back			
APPROVED		SIZE	CODE	DWG NO	REV
CHECKED		A			
DRAWN	Jacob Ganzer	4/2/2025	SCALE 1:2	WEIGHT	SHEET 25/26

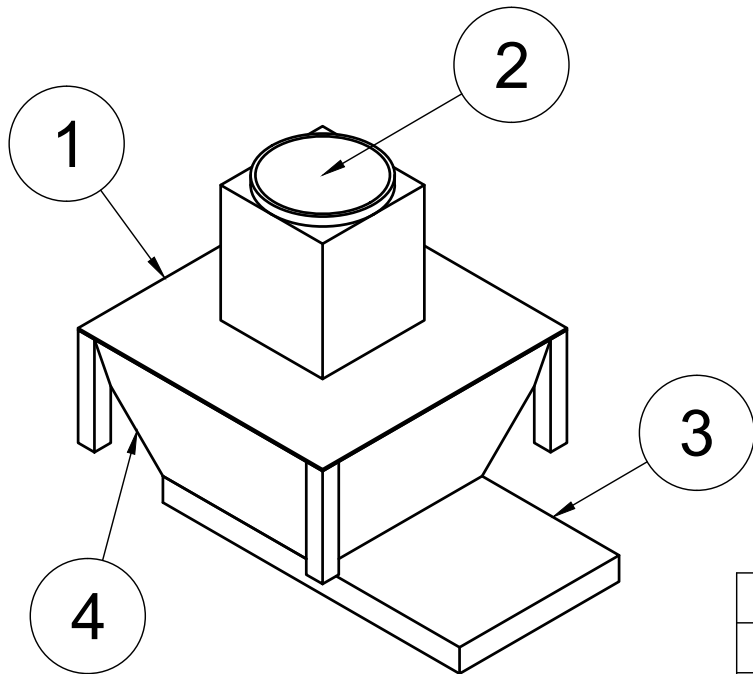

NOTES:

This assembly already exists on the current structure. No changes should be necessary

PARTS LIST			
ITEM	QTY	PART NUMBER	DESCRIPTION
1	1	CVD-S36	HOPPER COVER WITH BULK BAG INTERFACE CHUTE
2	1	IVM-12	12 INCH DIAMETER IRIS VALVE
3	1	VASM-SXXW-X	18" SQUARE MANUAL ROLLER GATE VALVE
4	1	HPX1-S36-X	SPECIAL TRANSITION HOPPER

		PROJECT		
		Bulk Bag Unloader		
		TITLE		
		Reused Components		
APPROVED		SIZE	CODE	DWG NO
CHECKED		A		
DRAWN	Jacob Ganzer	4/2/2025	SCALE 1:20	WEIGHT
				SHEET 26/26

ALL UNITS ARE IN INCHES