


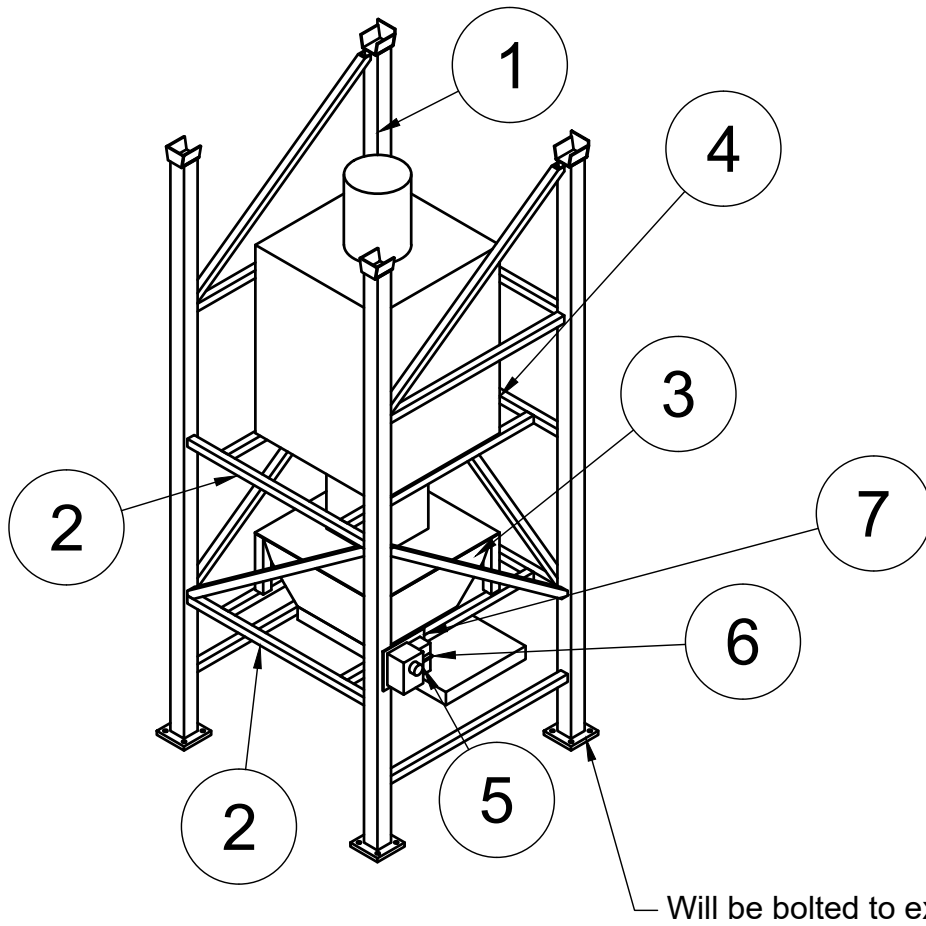



NOTES:

-Unless noted, all joints are to be welded

PARTS LIST		
ITEM	QTY	PART NAME
1	1	STRUCTURE
2	2	SUPPORT STRUCTURE
3	1	REUSED COMPONENTS V8
4	1	BAG V4
5	1	EMERGENCY STOP
6	1	SWITCH
7	1	ELECTRONICS MOUNT


ALL UNITS ARE IN
INCHES

		PROJECT			
		Bulk Bag Unloader			
		TITLE			
		Unloading System			
APPROVED		SIZE	CODE	DWG NO	REV
CHECKED		A			
DRAWN	Jacob Ganzer	4/2/2025	SCALE 1:40	WEIGHT	SHEET 1/31

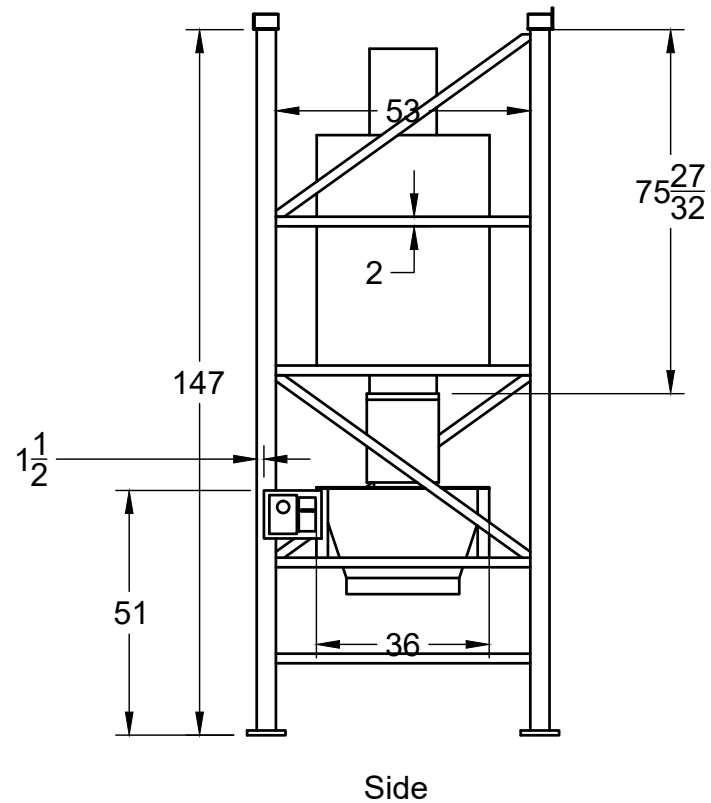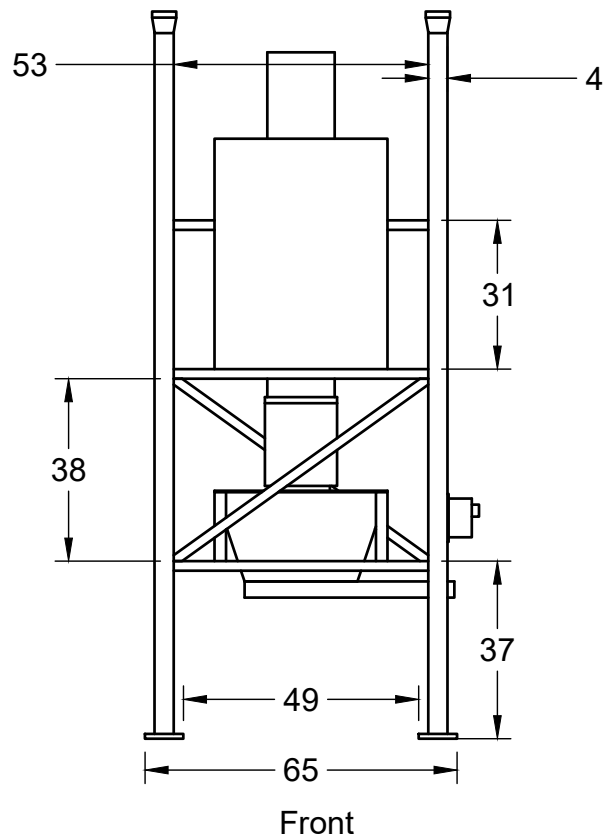

ALL UNITS ARE IN
INCHES


	PROJECT						
	Bulk Bag Unloader						
	TITLE						
	Unloading System						
APPROVED	SIZE		CODE		DWG NO		REV
CHECKED	A						
DRAWN	Jacob Ganzer	4/2/2025	SCALE 1:40		WEIGHT		SHEET 2/31

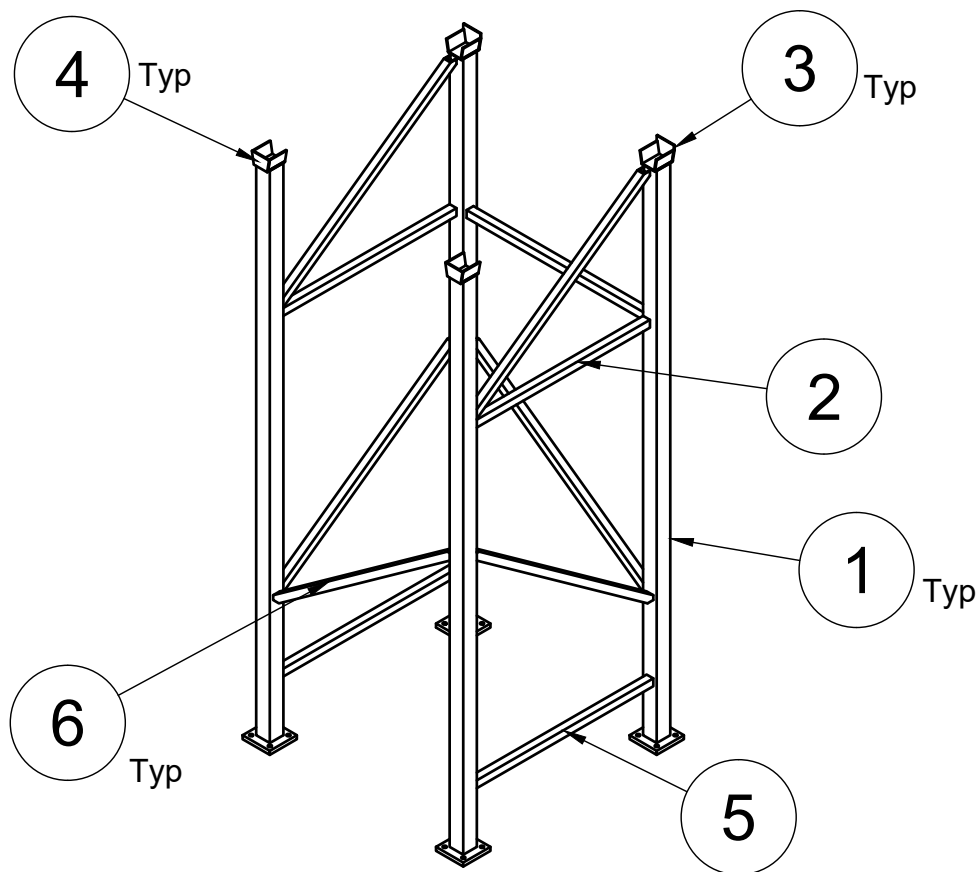

PARTS LIST		
ITEM	QTY	PART NAME
1	4	UPRIGHT STRUCTURE
2	1	BAG BRACE
3	2	UPRIGHT BACK CAP
4	2	UPRIGHT FRONT CAP
5	1	BASE BRACE
6	6	STRUCTURAL BAR D

ALL UNITS ARE IN
INCHES


		PROJECT		
		Bulk Bag Unloader		
		TITLE		
		Structure		
APPROVED		SIZE	CODE	DWG NO
CHECKED		A		
DRAWN	Jacob Ganzer	4/2/2025	SCALE 1:60	WEIGHT
			SHEET 3/31	

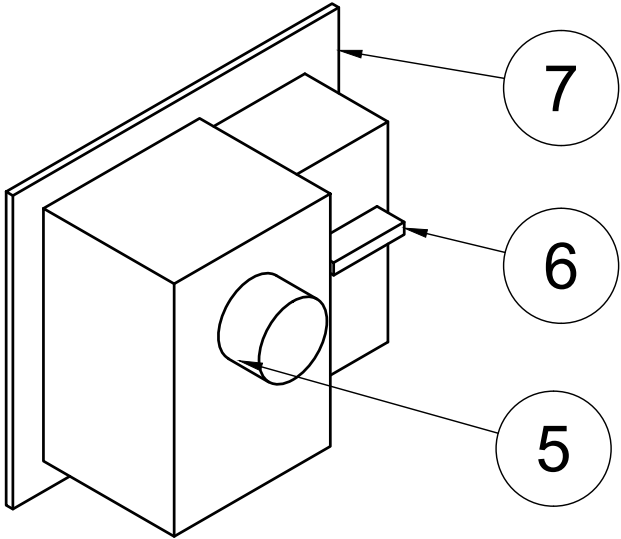

PARTS LIST			
ITEM	QTY	PART NAME	MATERIAL
5	1	EMERGENCY STOP	STEEL
6	1	SWITCH	STEEL
7	1	ELECTRONICS MOUNT	STEEL ASTM A36

		PROJECT			
		Bulk Bag Unloader			
		TITLE			
		Electronics Panel			
APPROVED		SIZE	CODE	DWG NO	REV
CHECKED		A			
DRAWN	Jacob Ganzer	4/2/2025	SCALE 1:5	WEIGHT	SHEET 4/31


ALL UNITS ARE IN INCHES

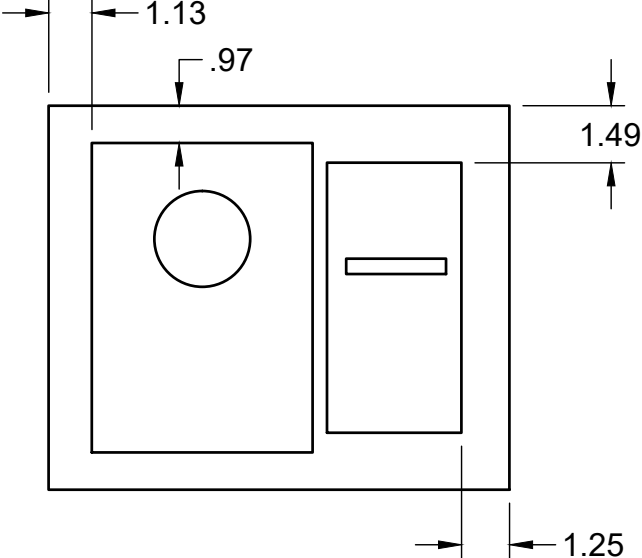


Front

ALL UNITS ARE IN
INCHES

		PROJECT			
		Bulk Bag Unloader			
		TITLE			
		Electronics Panel			
APPROVED		SIZE	CODE	DWG NO	REV
CHECKED		A			
DRAWN	Jacob Ganzer	4/2/2025	SCALE 1:5	WEIGHT	SHEET 5/31

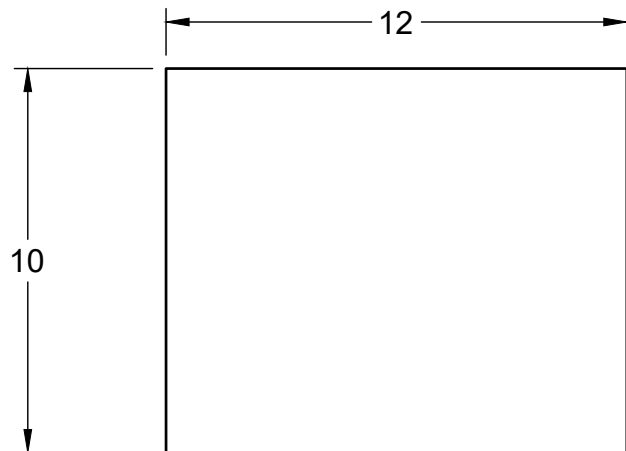

Front

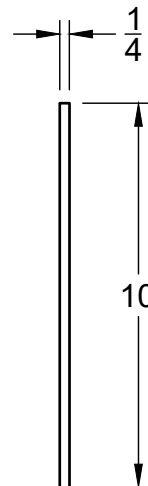


Side

Notes:

This component is meant to be welded to the base of the Unloading Structure

ALL UNITS ARE IN INCHES


		PROJECT			
		Bulk Bag Unloader			
		TITLE			
		Electronics Panel			
APPROVED		SIZE	CODE	DWG NO	REV
CHECKED		A			
DRAWN	Jacob Ganzer	4/2/2025	SCALE 1:5	WEIGHT	SHEET 6/31

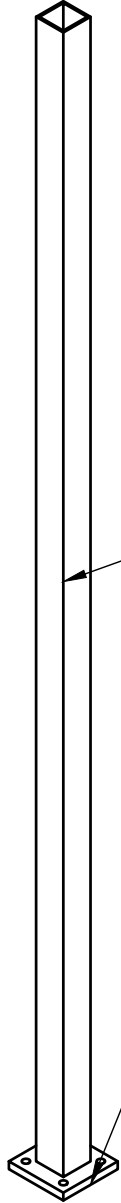

PARTS LIST				
ITEM	QTY	PART NAME	DESCRIPTION	MATERIAL
1	1	UPRIGHT SUPPORT	4"X4" TUBING	STEEL ASTM A500 GR B
2	1	BASE MOUNT	1" PLATE	STEEL ASTM A36


		PROJECT			
		Bulk Bag Unloader			
		TITLE			
		Upright Structure			
APPROVED		SIZE	CODE	DWG NO	REV
CHECKED		A			
DRAWN	Jacob Ganzer	4/2/2025	SCALE 1:20	WEIGHT	SHEET 7/31

ALL UNITS ARE IN
INCHES

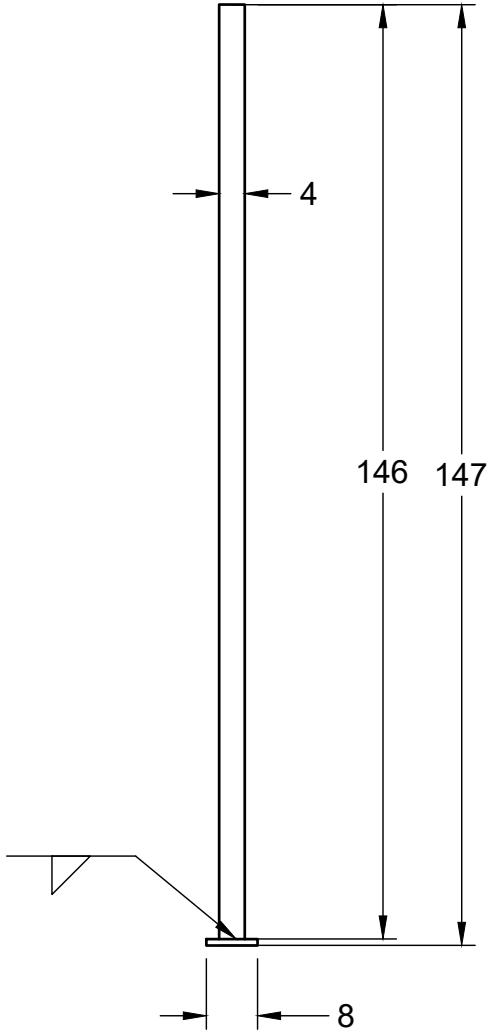


ALL UNITS ARE IN
INCHES

		PROJECT			
		Bulk Bag Unloader			
		TITLE			
		Upright Structure			
APPROVED		SIZE	CODE	DWG NO	REV
CHECKED		A			
DRAWN	Jacob Ganzer	4/2/2025	SCALE 1:20	WEIGHT	SHEET 8/31

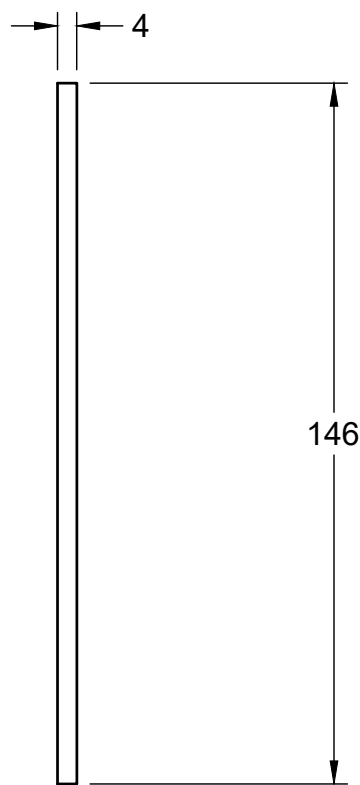



SCALE 1:40
Front

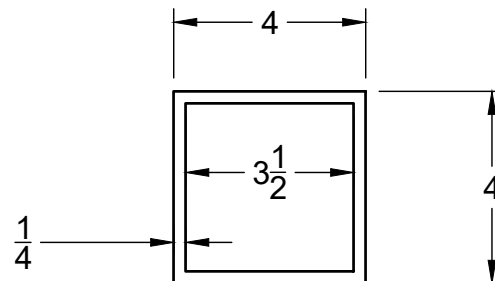

SCALE 1:4
Side


ALL UNITS ARE IN
INCHES

		PROJECT			
		Bulk Bag Unloader			
		TITLE			
		Upright Support			
APPROVED		SIZE	CODE	DWG NO	REV
CHECKED		A			
DRAWN	Jacob Ganzer	4/2/2025	SCALE 1:40	WEIGHT	SHEET 9/31

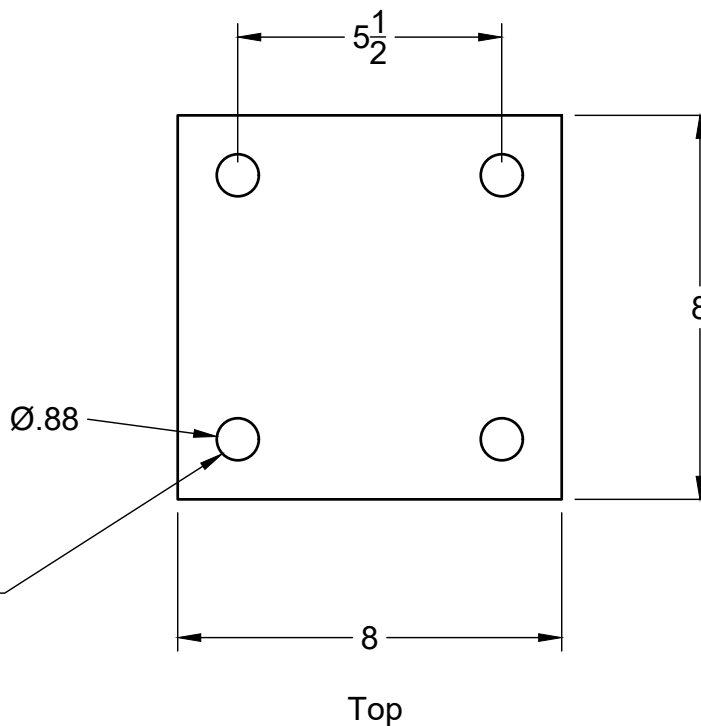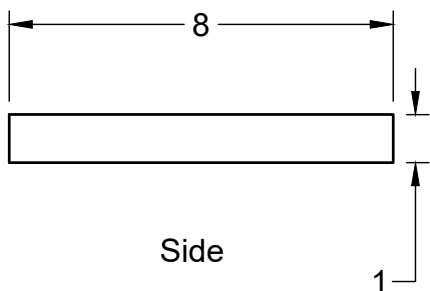

ALL UNITS ARE IN
INCHES

		PROJECT			
		Bulk Bag Unloader			
		TITLE			
		Upright Support Bottom			
APPROVED		SIZE	CODE	DWG NO	REV
CHECKED		A			
DRAWN	Jacob Ganzer	4/2/2025	SCALE 1:4	WEIGHT	SHEET 10/31

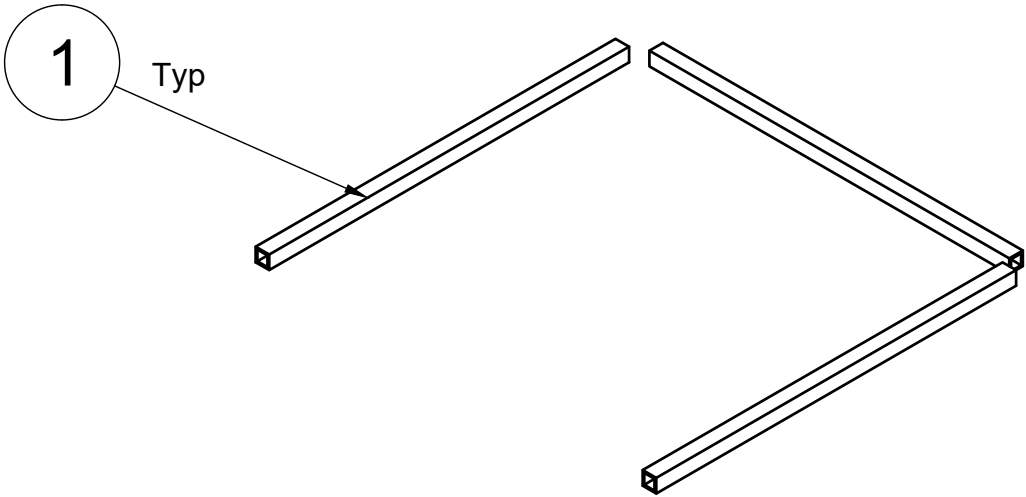


NOTES:

All joints are to be welded

PARTS LIST			
ITEM	QTY	PART NUMBER	MATERIAL
1	3	STRUCTURAL BAR C	STEEL ASTM A500 GR B

	PROJECT				
	Bulk Bag Unloader				
	TITLE				
	Bag Brace				
APPROVED	SIZE	CODE	DWG NO		REV
CHECKED	A				
DRAWN	Jacob Ganzer	4/2/2025	SCALE 1:20	WEIGHT	SHEET 11/31

ALL UNITS ARE IN INCHES

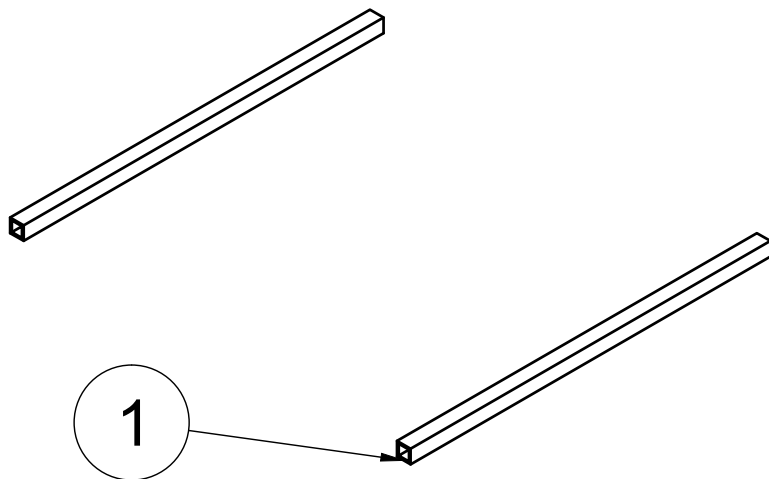


NOTES:

All joints are to be welded


PARTS LIST			
ITEM	QTY	PART NUMBER	MATERIAL
1	2	STRUCTURAL BAR C	STEEL ASTM A500 GR B

		PROJECT		
		Bulk Bag Unloader		
		TITLE		
		Base Brace		
APPROVED		SIZE	CODE	DWG NO
CHECKED		A		
DRAWN	Jacob Ganzer	4/2/2025	SCALE 1:20	WEIGHT
			SHEET 12/31	

ALL UNITS ARE IN
INCHES

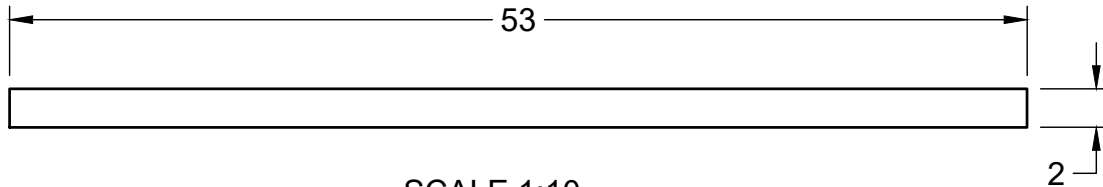


SCALE 1:10
Front

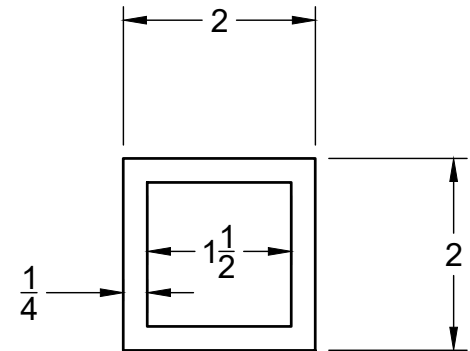

SCALE 1:2
Side

ALL UNITS ARE IN
INCHES



	PROJECT			
	Bulk Bag Unloader			
	TITLE			
	Structural Bar C			
APPROVED	SIZE	CODE	DWG NO	REV
CHECKED	A			
DRAWN	Jacob Ganzer	4/2/2025	SCALE 1:10	WEIGHT
			SHEET	13/31

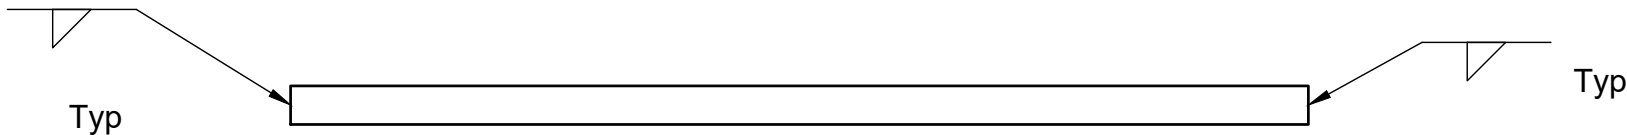


Side

ALL UNITS ARE IN
INCHES


		PROJECT			
		Bulk Bag Unloader			
		TITLE			
		Structural Bar C			
APPROVED		SIZE	CODE	DWG NO	REV
CHECKED		A			
DRAWN	Jacob Ganzer	4/2/2025	SCALE 1:10	WEIGHT	SHEET 14/31

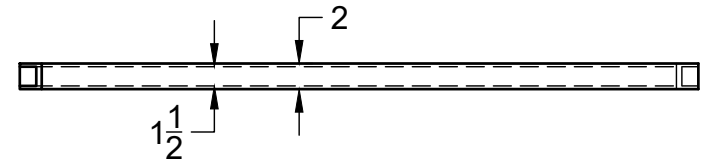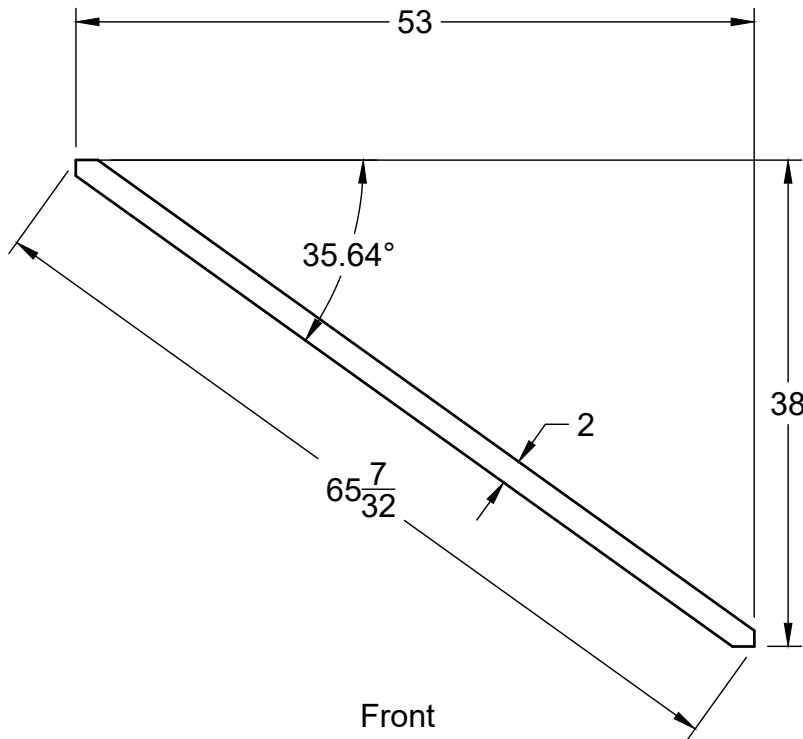

PARTS LIST					
ITEM	QTY	PART NAME	DESCRIPTION		MATERIAL
6	1	STRUCTURAL BAR D	2"X2"X1/4" TUBING		STEEL ASTM A500 GR B
			PROJECT		
			Bulk Bag Unloader		
			TITLE		
			Structural Bar D		
APPROVED			SIZE	CODE	DWG NO
CHECKED			A		
DRAWN			SCALE 1:15		REV
Jacob Ganzer 4/2/2025			WEIGHT		SHEET 15/31

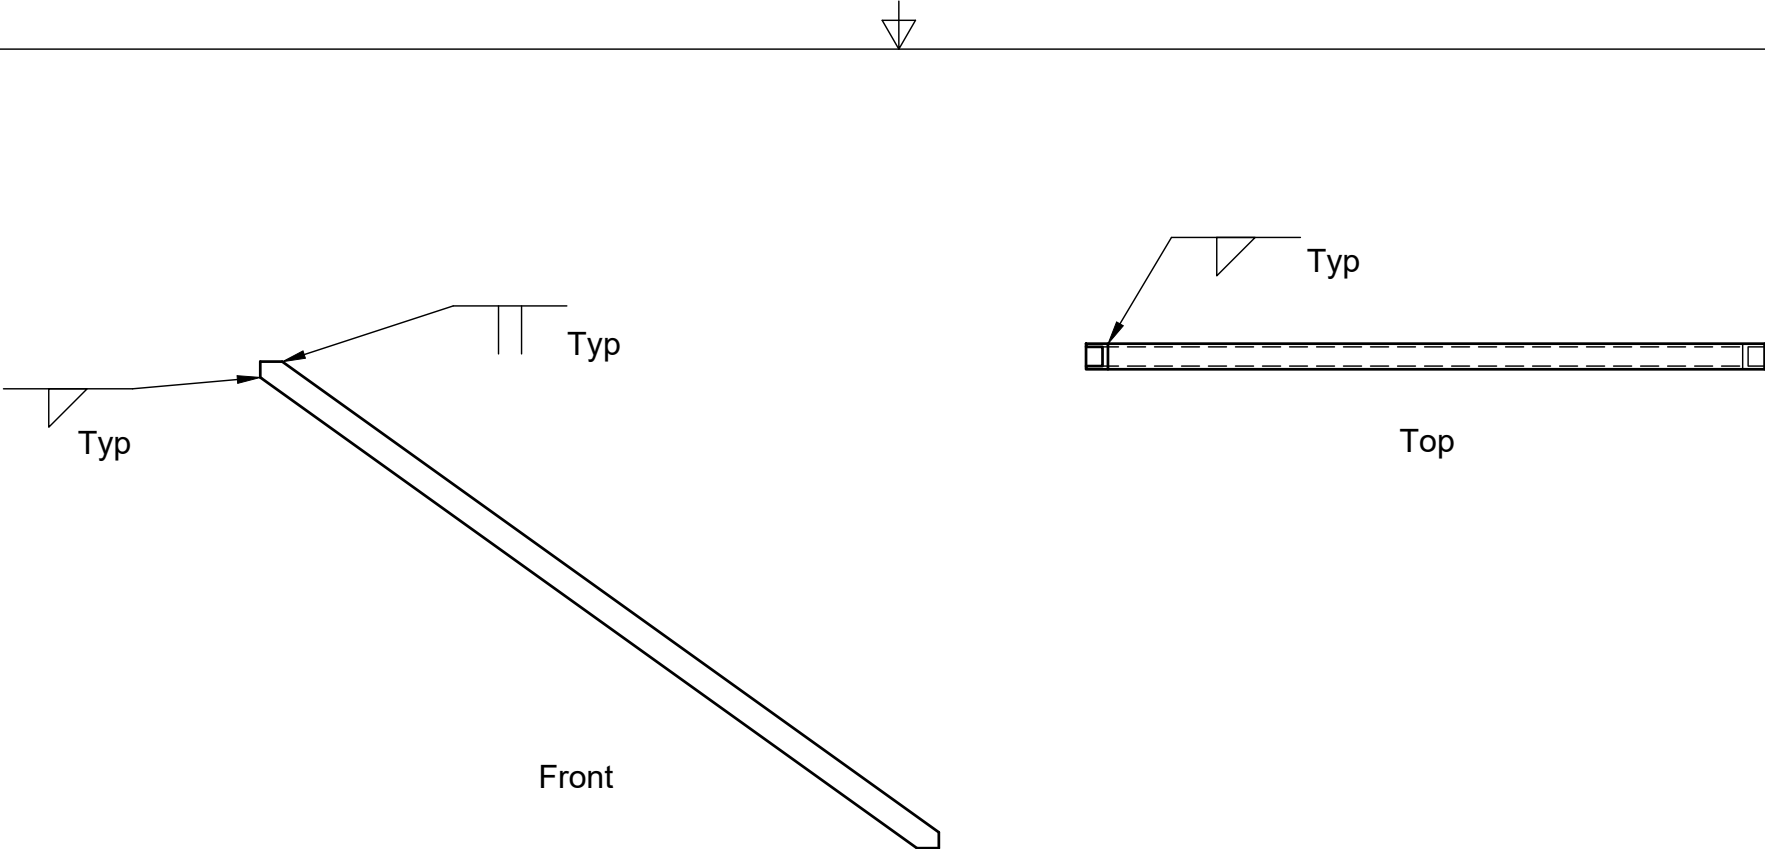

		PROJECT			
		Bulk Bag Unloader			
		TITLE			
		Structural Bar D			
APPROVED		SIZE	CODE	DWG NO	REV
CHECKED		A			
DRAWN	Jacob Ganzer	4/2/2025	SCALE 1:15	WEIGHT	SHEET 16/31

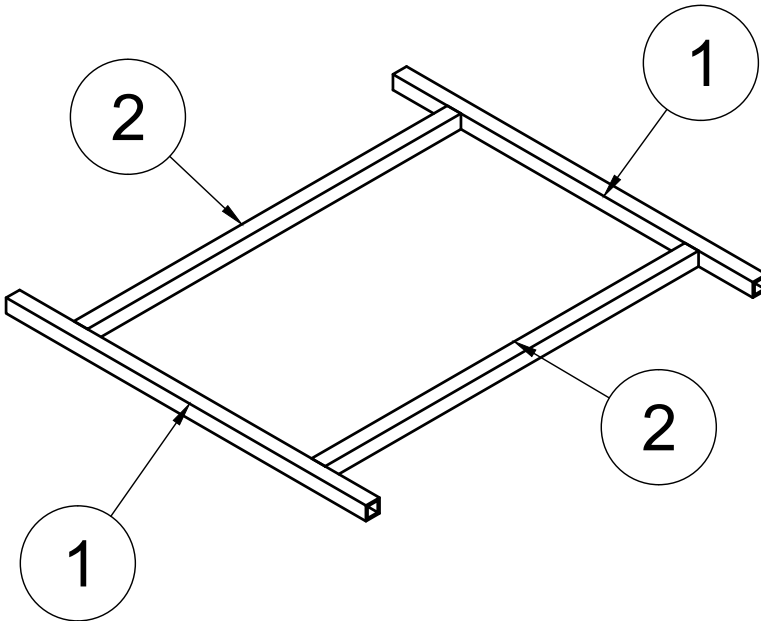


NOTES:

All joints are to be welded


PARTS LIST				
ITEM	QTY	PART NAME	DESCRIPTION	MATERIAL
1	2	STRUCTURAL BAR A	2"X2" TUBING	STEEL ASTM A500 GR B
2	2	STRUCTURAL BAR B	2"X2" TUBING	STEEL ASTM A500 GR B

		PROJECT		
		Bulk Bag Unloader		
		TITLE		
		Support Structure		
APPROVED		SIZE	CODE	DWG NO
CHECKED		A		
DRAWN	Jacob Ganzer	4/2/2025	SCALE 1:20	WEIGHT
			SHEET 17/31	

ALL UNITS ARE IN INCHES

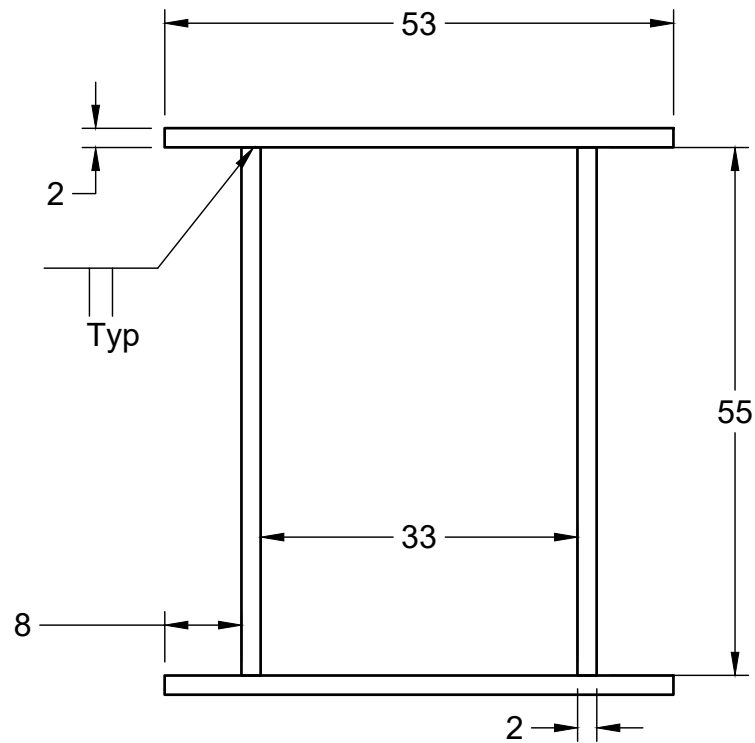

Top


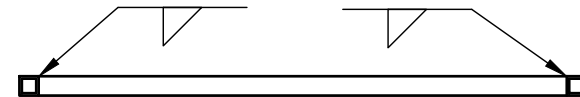


Side

ALL UNITS ARE IN
INCHES

		PROJECT			
		Bulk Bag Unloader			
		TITLE			
		Support Structure			
APPROVED		SIZE	CODE	DWG NO	REV
CHECKED		A			
DRAWN	Jacob Ganzer	4/2/2025	SCALE 1:20	WEIGHT	SHEET 18/31



Front

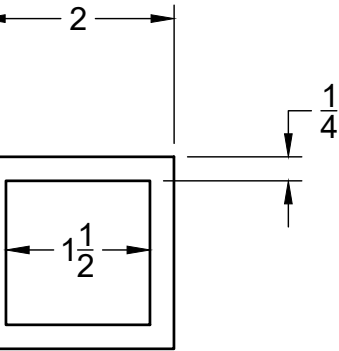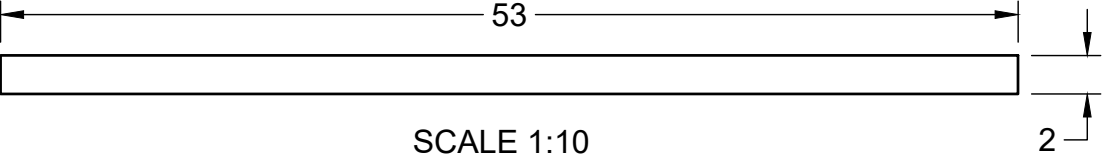

SCALE 1:2
Side


ALL UNITS ARE IN
INCHES

		PROJECT			
		Bulk Bag Unloader			
		TITLE			
		Structural Bar A			
APPROVED		SIZE	CODE	DWG NO	REV
CHECKED		A			
DRAWN	Jacob Ganzer	4/2/2025	SCALE 1:10	WEIGHT	SHEET 19/31

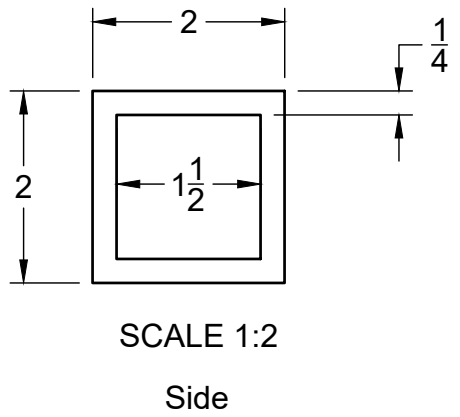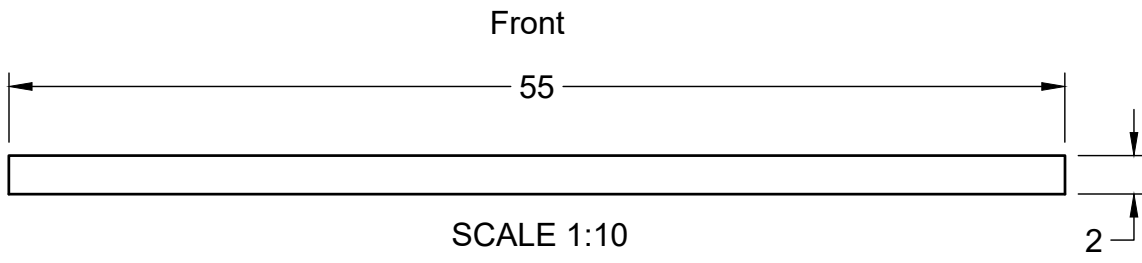

ALL UNITS ARE IN
INCHES

		PROJECT			
		Bulk Bag Unloader			
		TITLE			
		Structural Bar B			
APPROVED		SIZE	CODE	DWG NO	REV
CHECKED		A			
DRAWN	Jacob Ganzer	4/2/2025	SCALE 1:10	WEIGHT	SHEET 20/31

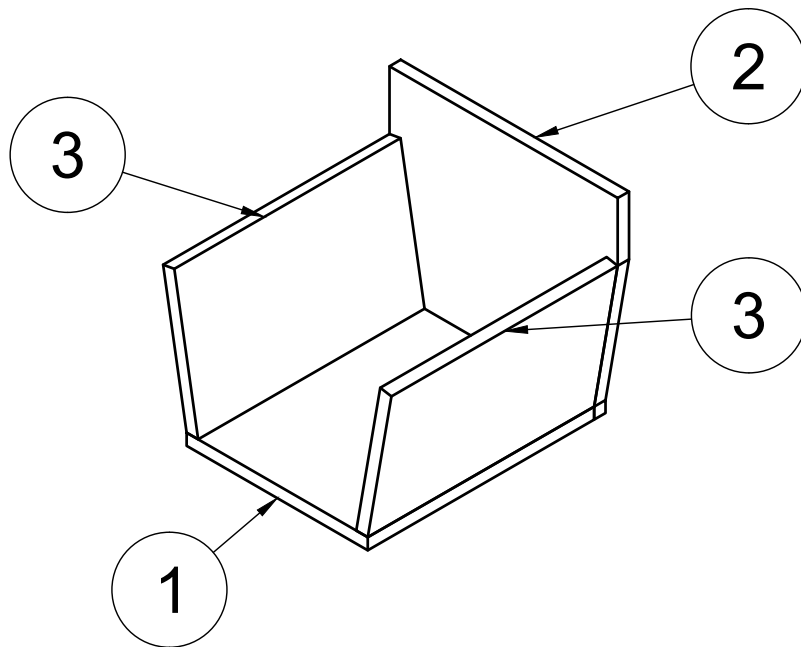


NOTES:

All joints are to be welded


PARTS LIST				
ITEM	QTY	PART NAME	DESCRIPTION	MATERIAL
1	1	CAP BASE	1/4" PLATE	STEEL ASTM A36
2	1	TALL BACK	1/4" PLATE	STEEL ASTM A36
3	2	CAP SIDE	1/4" PLATE	STEEL ASTM A36

		PROJECT			
		Bulk Bag Unloader			
		TITLE			
		Upright Back Cap			
APPROVED		SIZE	CODE	DWG NO	REV
CHECKED		A			
DRAWN	Jacob Ganzer	4/2/2025	SCALE 1:3	WEIGHT	SHEET 21/31

ALL UNITS ARE IN
INCHES

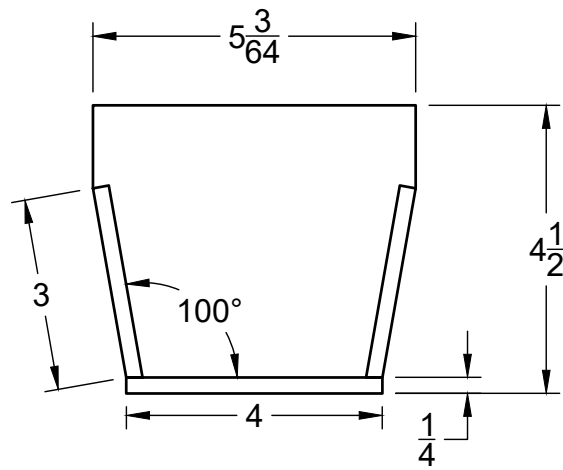


Front

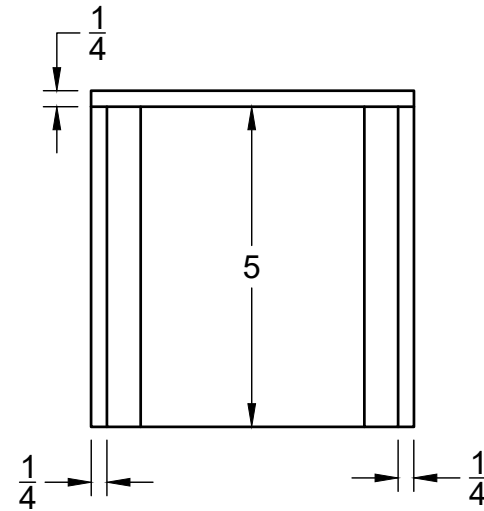


Top

ALL UNITS ARE IN
INCHES

		PROJECT			
		Bulk Bag Unloader			
		TITLE			
		Upright Back Cap			
APPROVED		SIZE	CODE	DWG NO	REV
CHECKED		A			
DRAWN	Jacob Ganzer	4/2/2025	SCALE 1:3	WEIGHT	SHEET 22/31

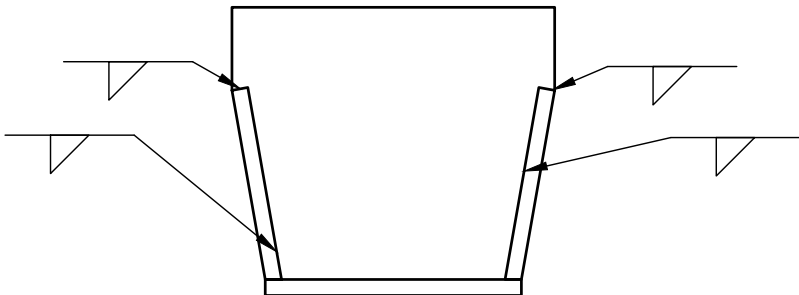


Front

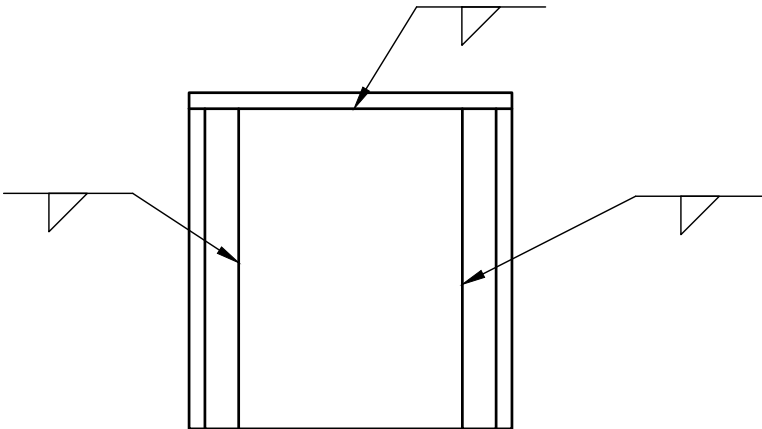

Top

ALL UNITS ARE IN
INCHES

		PROJECT			
		Bulk Bag Unloader			
		TITLE			
		Upright Back Cap			
APPROVED		SIZE	CODE	DWG NO	REV
CHECKED		A			
DRAWN	Jacob Ganzer	4/2/2025	SCALE 1:3	WEIGHT	SHEET 23/31

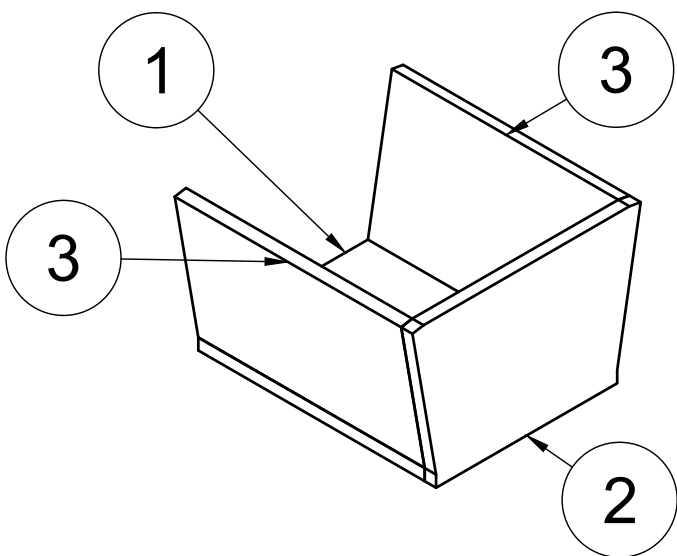


NOTES:

All joints are to be welded


PARTS LIST				
ITEM	QTY	PART NAME	DESCRIPTION	MATERIAL
1	1	CAP BASE	1/4" PLATE	STEEL ASTM A36
2	1	SHORT BACK	1/4" PLATE	STEEL ASTM A36
3	2	CAP SIDE	1/4" PLATE	STEEL ASTM A36

		PROJECT		
		Bulk Bag Unloader		
		TITLE		
		Upright Front Cap		
APPROVED		SIZE	CODE	DWG NO
CHECKED		A		
DRAWN	Jacob Ganzer	4/2/2025	SCALE 1:3	WEIGHT
			SHEET 24/31	

ALL UNITS ARE IN INCHES

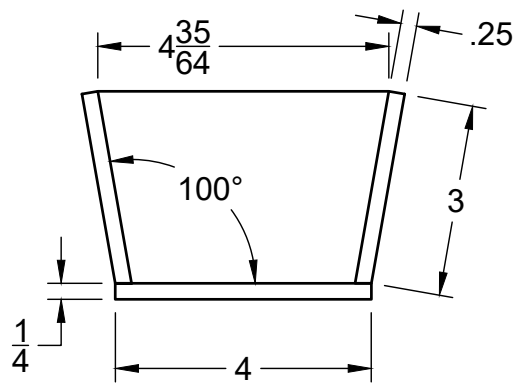


Front

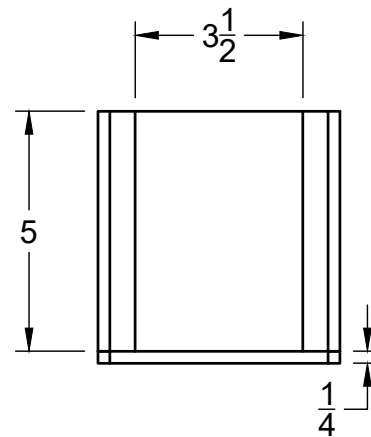


Top

ALL UNITS ARE IN
INCHES

		PROJECT			
		Bulk Bag Unloader			
		TITLE			
		Upright Front Cap			
APPROVED		SIZE	CODE	DWG NO	REV
CHECKED		A			
DRAWN	Jacob Ganzer	4/2/2025	SCALE 1:3	WEIGHT	SHEET 25/31

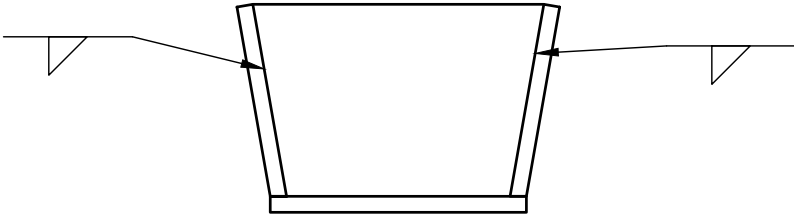


Front

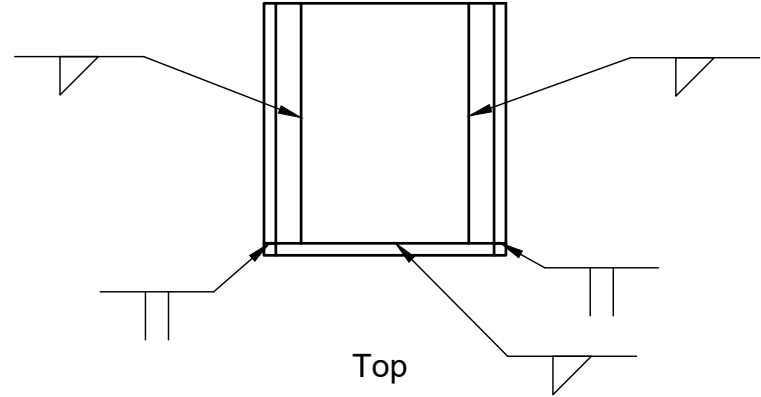


Top

ALL UNITS ARE IN
INCHES

		PROJECT			
		Bulk Bag Unloader			
		TITLE			
		Upright Front Cap			
APPROVED		SIZE	CODE	DWG NO	REV
CHECKED		A			
DRAWN	Jacob Ganzer	4/2/2025	SCALE 1:3	WEIGHT	SHEET 26/31

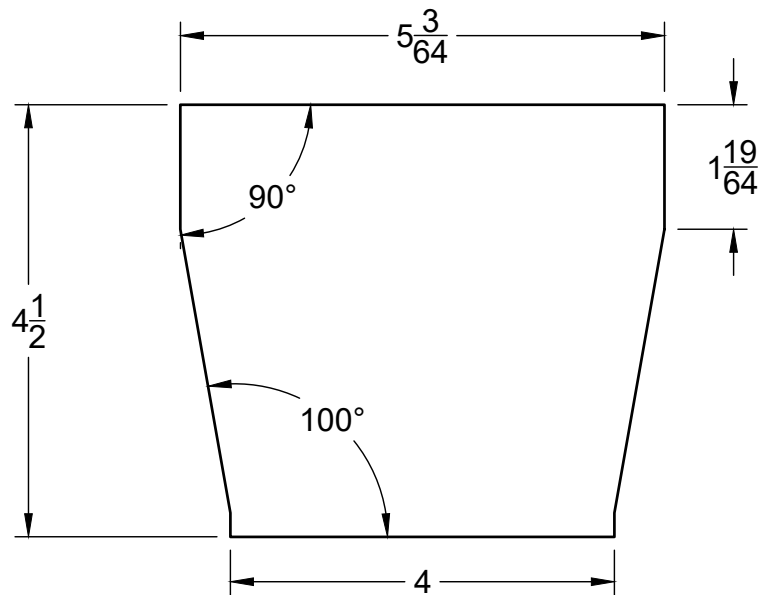


Front

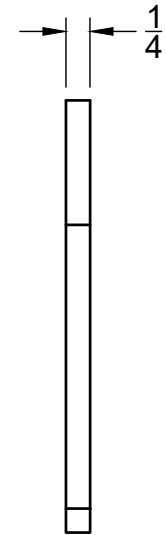


Side

ALL UNITS ARE IN
INCHES

	PROJECT				
	Bulk Bag Unloader				
	TITLE				
	Tall Back				
APPROVED	SIZE	CODE	DWG NO		REV
CHECKED	A				
DRAWN	Jacob Ganzer	4/2/2025	SCALE 1:2	WEIGHT	SHEET 27/31

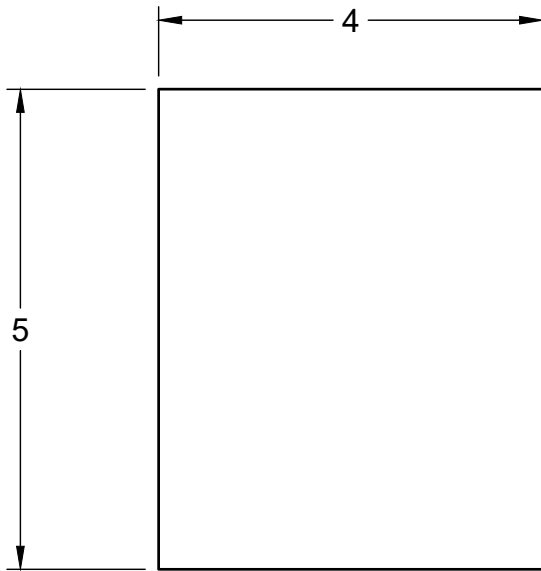


Top

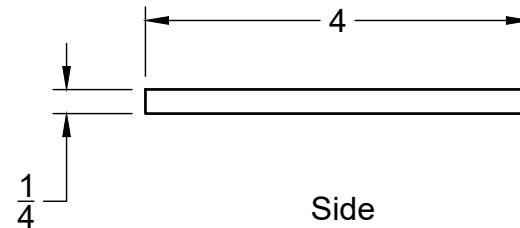


Side

ALL UNITS ARE IN
INCHES

		PROJECT			
		Bulk Bag Unloader			
		TITLE			
		Cap Base			
APPROVED		SIZE	CODE	DWG NO	REV
CHECKED		A			
DRAWN	Jacob Ganzer	4/2/2025	SCALE 1:2	WEIGHT	SHEET 28/31

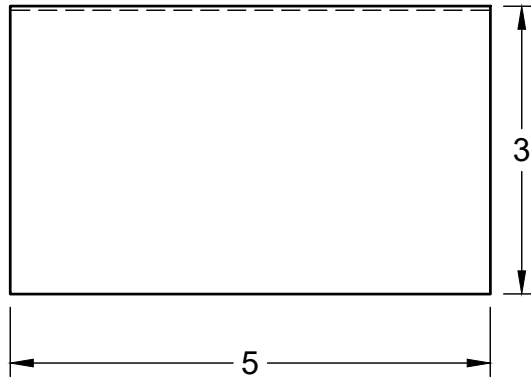


Bottom

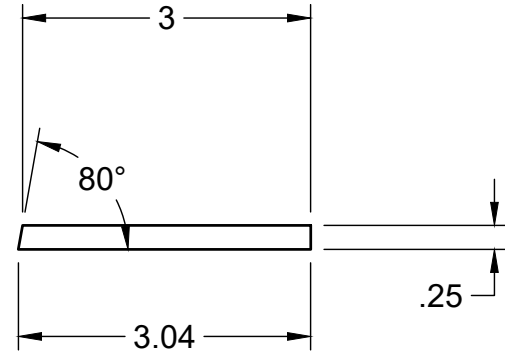


Side

ALL UNITS ARE IN
INCHES

				PROJECT			
				Bulk Bag Unloader			
				TITLE			
				Cap Side			
APPROVED				SIZE	CODE	DWG NO	REV
CHECKED				A			
DRAWN	Jacob Ganzer	4/2/2025	SCALE	1:2	WEIGHT	SHEET 29/31	

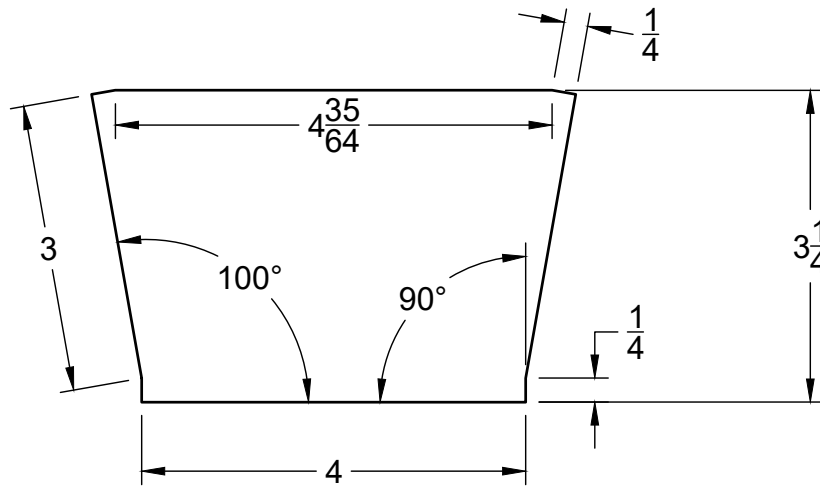


Front

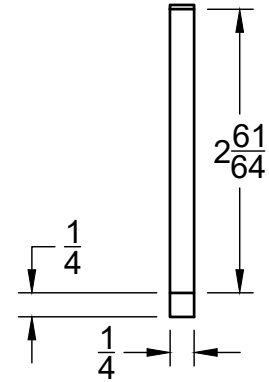

Side

ALL UNITS ARE IN
INCHES

		PROJECT			
		Bulk Bag Unloader			
		TITLE			
		Short Back			
APPROVED		SIZE	CODE	DWG NO	REV
CHECKED		A			
DRAWN	Jacob Ganzer	4/2/2025	SCALE 1:2	WEIGHT	SHEET 30/31

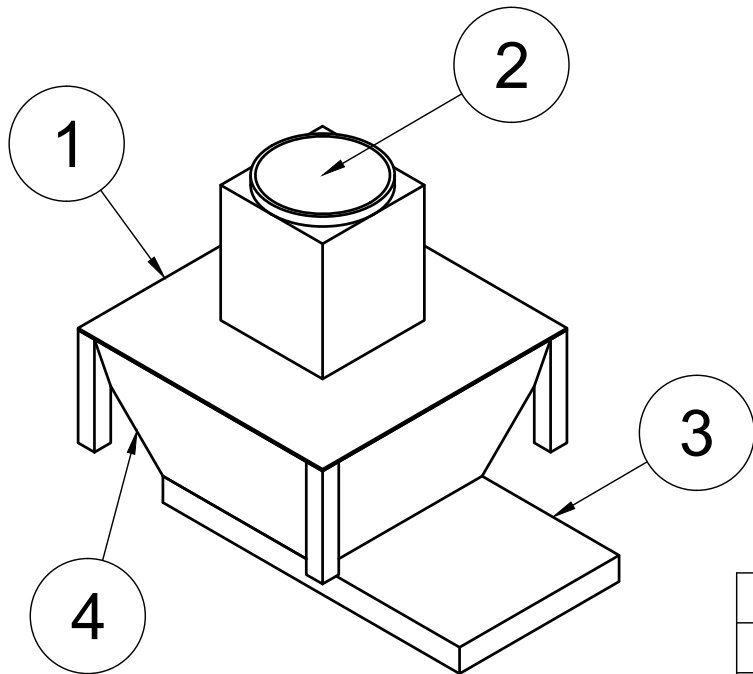

NOTES:

This assembly already exists on the current structure. No changes should be necessary

PARTS LIST			
ITEM	QTY	PART NUMBER	DESCRIPTION
1	1	CVD-S36	HOPPER COVER WITH BULK BAG INTERFACE CHUTE
2	1	IVM-12	12 INCH DIAMETER IRIS VALVE
3	1	VASM-SXXW-X	18" SQUARE MANUAL ROLLER GATE VALVE
4	1	HPX1-S36-X	SPECIAL TRANSITION HOPPER

		PROJECT		
		Bulk Bag Unloader		
		TITLE		
		Reused Components		
APPROVED		SIZE	CODE	DWG NO
CHECKED		A		
DRAWN	Jacob Ganzer	4/2/2025	SCALE 1:20	WEIGHT
				SHEET 31/31

ALL UNITS ARE IN INCHES