


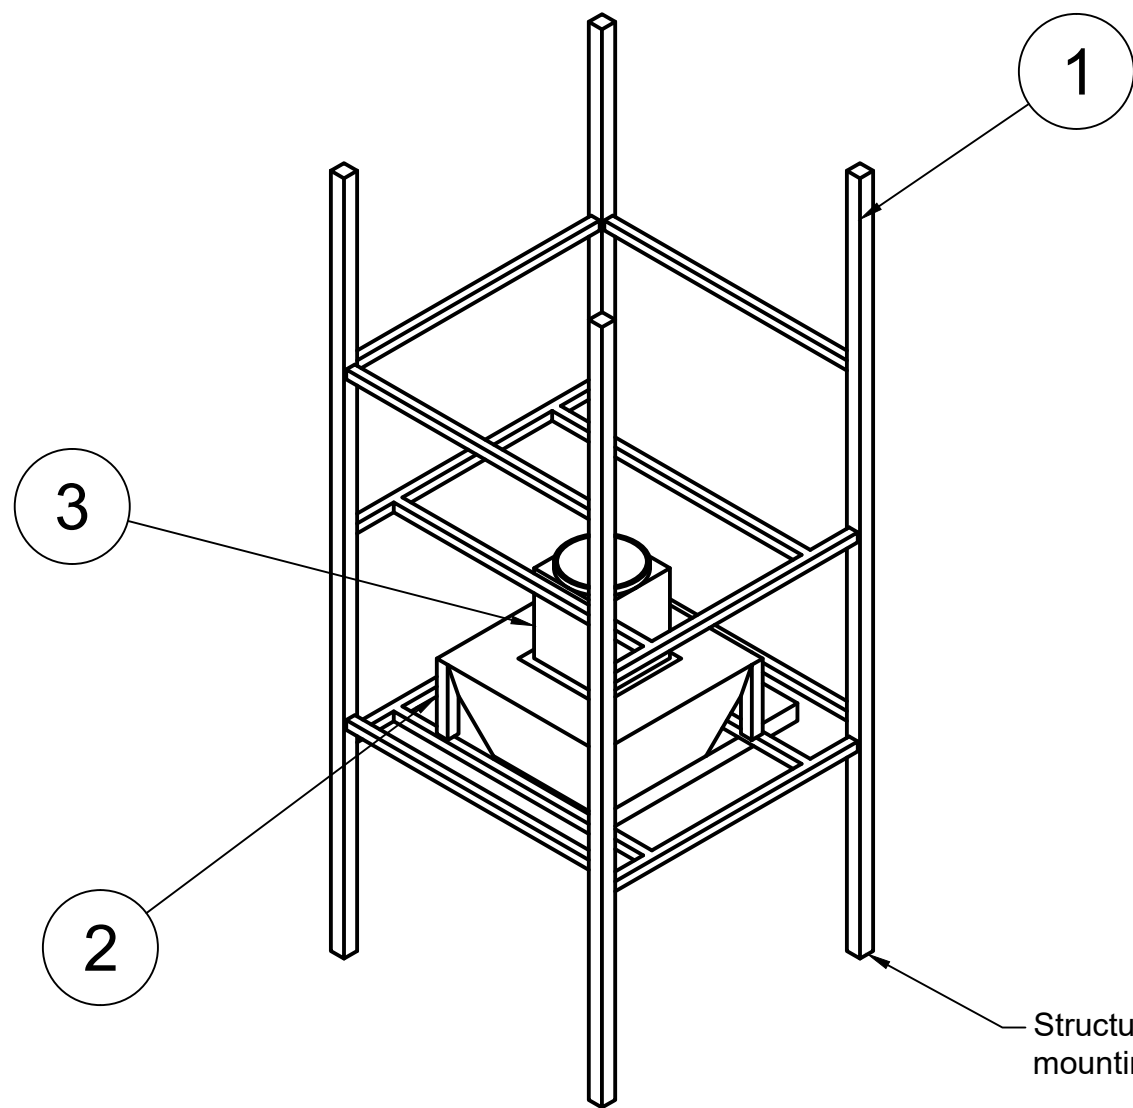

Notes:

-Parts 2 and 3 have been salvaged from the existing structure



-Unless noted otherwise, all joints are to be welded

Structure will be bolted to the pad using the existing mounting hardware

| PARTS LIST |                                 |
|------------|---------------------------------|
| ITEM       | PART NUMBER                     |
| 1          | SUPPORT STRUCTURE               |
| 2          | SLIDE VALVE AND HOPPER ASSEMBLY |
| 3          | BAG CUTTER                      |

All dimensions are given in inches

|          |                   |           |            |        |
|----------|-------------------|-----------|------------|--------|
|          | PROJECT           |           |            |        |
|          | Bulk Bag Unloader |           |            |        |
|          | TITLE             |           |            |        |
|          | System            |           |            |        |
| APPROVED | SIZE              | CODE      | DWG NO     | REV    |
| CHECKED  | B                 |           |            |        |
| DRAWN    | Jacob Ganzer      | 3/26/2025 | SCALE 1:30 | WEIGHT |
|          |                   |           | SHEET 1/2  |        |

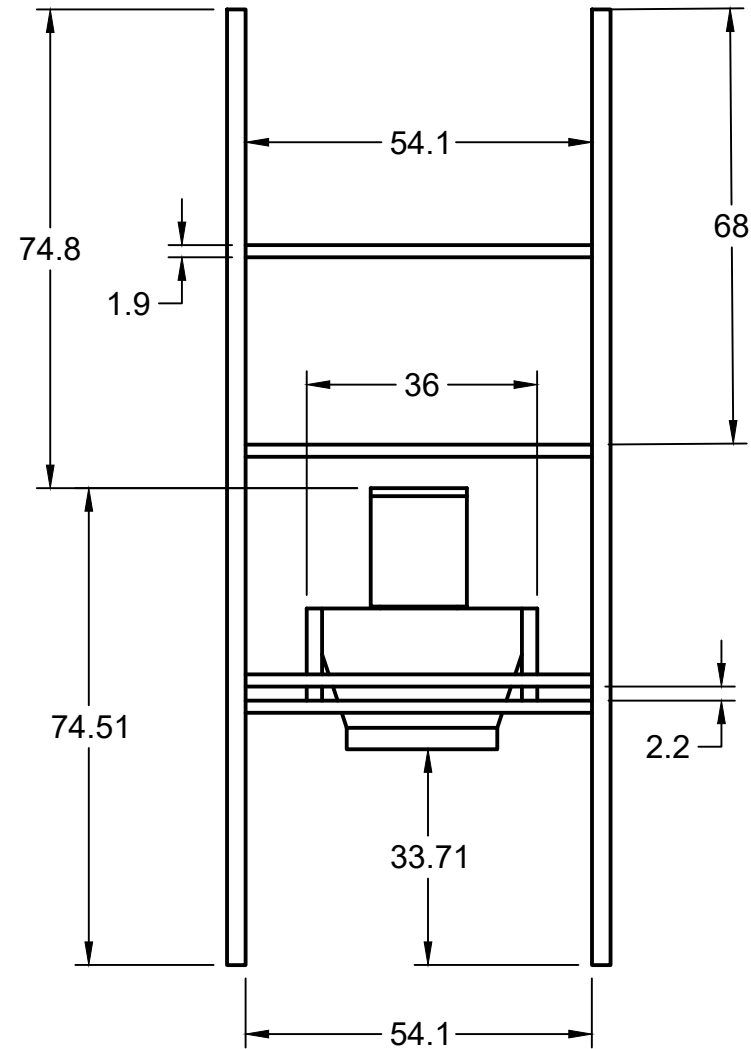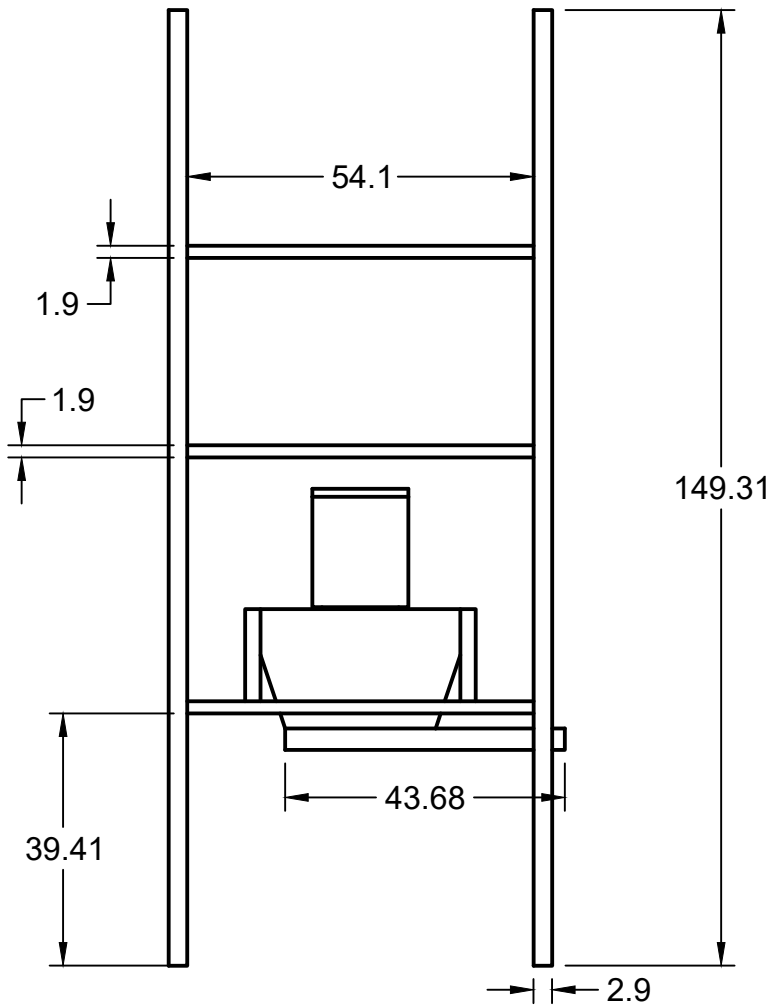

All dimensions are given  
in inches

|          |                              |           |            |        |
|----------|------------------------------|-----------|------------|--------|
|          | PROJECT<br>Bulk Bag Unloader |           |            |        |
|          | TITLE<br>System              |           |            |        |
| APPROVED | SIZE                         | CODE      | DWG NO     | REV    |
| CHECKED  | B                            |           |            |        |
| DRAWN    | Jacob Ganzer                 | 3/26/2025 | SCALE 1:30 | WEIGHT |
|          |                              |           | SHEET 2/2  |        |